



SISTEMA DE SEMÁFOROS INTELIGENTE (SSI) - BOGOTÁ D.C.
CONTRATO SDM 2017 1913

ACTA DE ENTREGA - PLANEAMIENTO SEMAFORICO

DATOS GENERALES		COMUNICACIONES		TIPO DE MODIFICACION	
NÚMERO EXTERNO:	3014	CONEXION:	Central	ESQUEMA:	NUEVA
EQUIPO:	C900V	PROTOCOLO:	OCIT2.0	MATRIZ CONFLICTOS:	NUEVA
ZONA PLANEAMIENTO:	Sur	FUNCIONAMIENTO:	BT-TE	MATRIZ INTERMEDIOS:	NUEVA
ZONA AUTOMÁTICA:	3524	TIPO DE PROGRAMACION LOGICA:	PDM	LÓGICA:	NUEVA
				T. FASES:	NUEVA
				PERMISIVIDAD:	NUEVA
				PARAMETROS TA:	
				PARAMETROS CA:	

DIRECCIÓN	FASES	DISPOSITIVOS	ESTADO DISPOSITIVOS	CONTADOR REGRESIVO
ID SIG: 1593	KR 24 X CL 55 SUR	4	Botón-Sonoro	Conectado - Conectado - N.A. - N.A.

CONTENIDO:	Cant.	Cant.	Cant.
Esquema	1	Tabla Detectores	1
Automático Interno (AI)	1	Parámetros TA	
Matriz de conflictos (MC)	1	Parámetros CA	
Matriz de Tiempos Intermedios (MI)	1	Tabla de Condiciones / Diagrama de Flujo	1
Plan de Conexión (PC)	1	Plan Secuencia de Fases (SF)	1
Plan de Desconexión (PD)	1	Transiciones de Fase (TF)	4
Planes de Señales (PS)	8	Planes de Permisividad (PP)	8

ACTIVIDAD	OBSERVACIONES:
Intersección Nueva	Se implementa intersección nueva y se incorpora a la zona automática 3524.


PROCESO	NOMBRE Y CARGO	FIRMA	FECHA
Elaboró CMF 2050:	Edwin Sotelo Palacios - Ing. Planeamiento de tráfico	Edwin Sotelo Palacios 2020.11.12 12:17:27 -05'00'	11/11/2020
Revisó y Aprobó CMF 2050:	Carlos Eduardo González Zuluaga - Ing. Especialista Tránsito y Transporte	Firmado digitalmente por Gonzalez Zuluaga Carlos Eduardo Fecha: 2020.11.12 12:34:22 -05'00'	11/11/2020
Aprobó CPT:	Herver Varela Mafla - Ing. Especialista Tránsito y Transporte	Firmado digitalmente por HERVER VARELA Fecha: 2020.11.19 17:03:32 -05'00'	
Validó SDM:		Douglas A. González P. 2020.11.23 08:14:01 -05'00'	

CONVENCIONES	Modo Local:	Modo Central:
	TF: Tiempos Fijos - TA: Tráfico Actuado	CA: Central Adaptativa - R: Responsivo - RP: Responsivo Pasivo - BT: Basado Tiempo

* para programación SL, los parametros se encuentran en la SF.

OPERACIONES - CMF 2050	
Coordinador	Operador
Nombre y Firma	Nombre y Firma
Fecha Implementación:	14/11/2021

Mapa

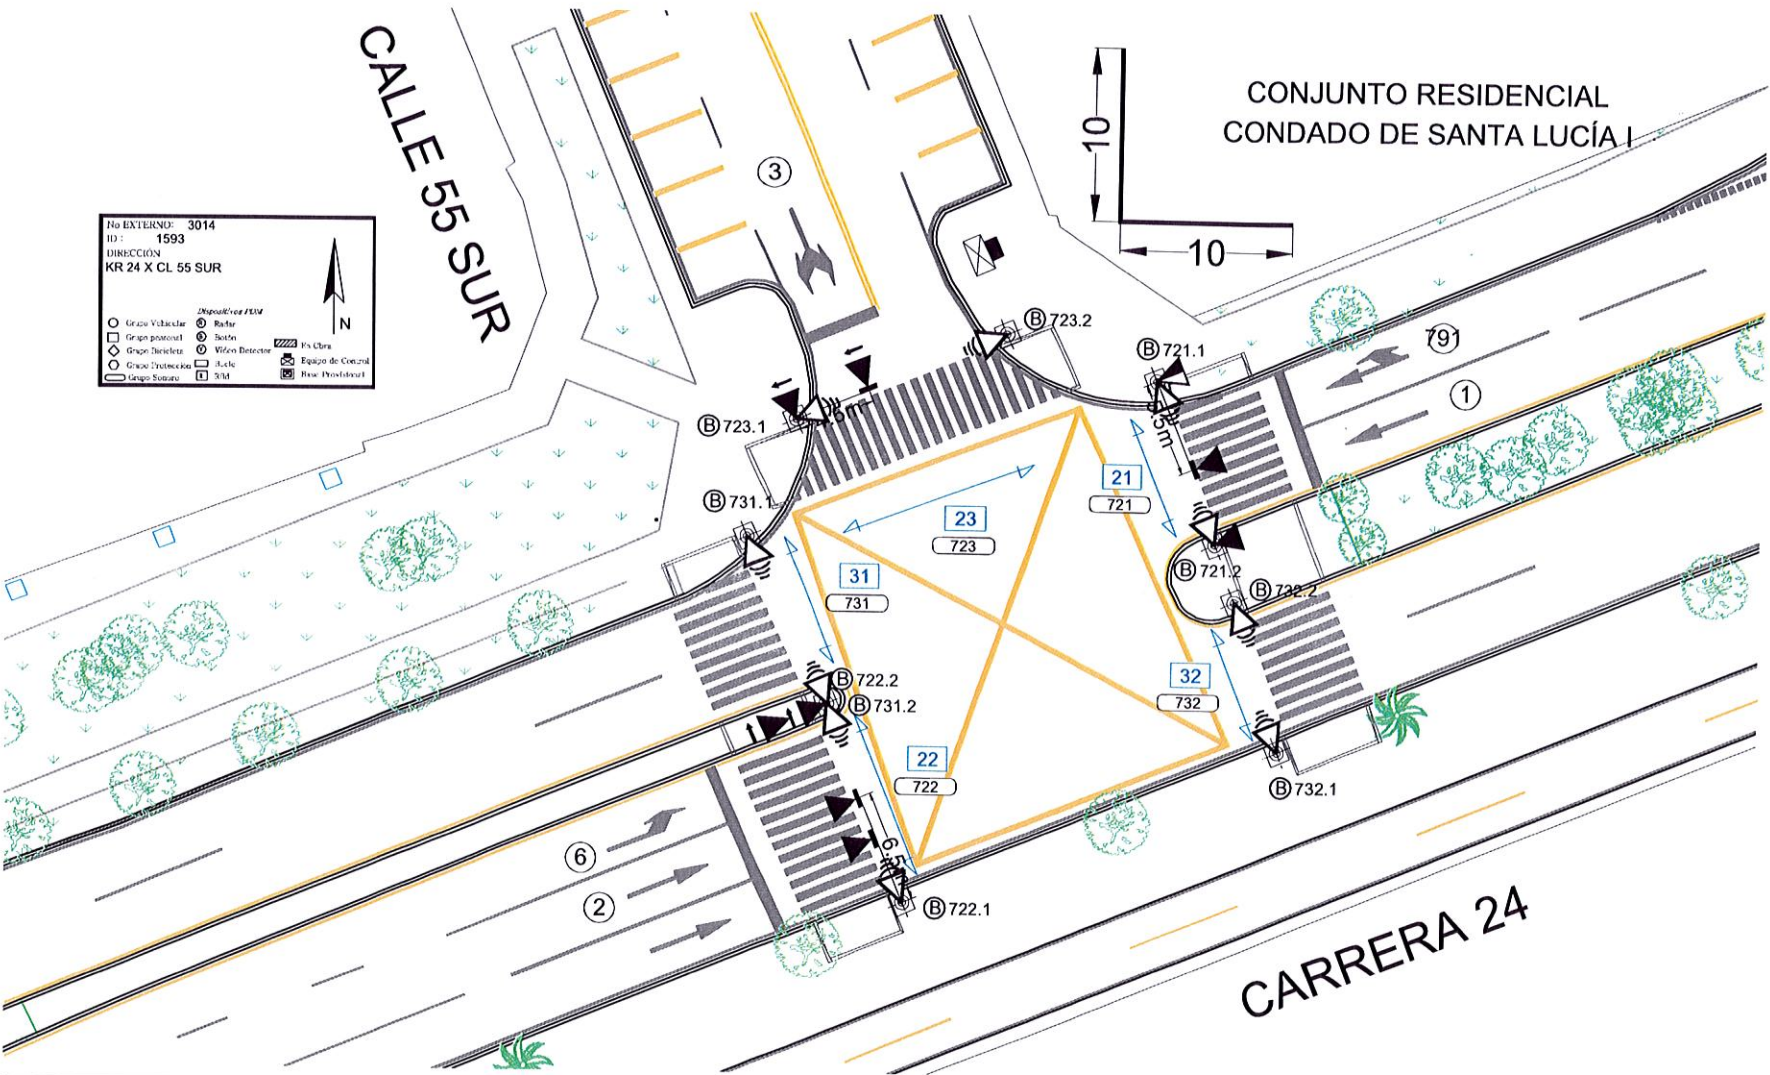

Externo:	3014	Dirección:	KR 24 X CL 55 SUR	Zona Auto:	3524	Vo.Bo.CMF	ING. CEGZ
Encargado:	Ing. Edwin Sotelo Palacios	Versión:	SSI_3014_Versión1.sop6	Fecha:	22/10/2020 11:31:52	Vo.Bo.CPT	
Contrato:	CTO SDM: 20171913	Consorcio Movilidad Futura 2050		Sittraffic Office		Vo.Bo.SDM	

Datos relevantes de seguridad \ Referencias del grupo de señales

Matrices de conflicto:

N.º	Nombre	Nombre corto	Descripción
1	MC_C900V_3014	MC_C900V_3014	

	GS de entrada	1	2	3	4	5	6	7	8	9	10	11	12	13	14	15
GS de despeje		1	2	3	6	791	21	22	23	31	32	721	722	723	731	732
1	1			X	X		X			X		X			X	
2	2			X				X			X		X			X
3	3	X	X		X	X			X	X	X				X	X
4	6	X		X		X		X	X				X	X		
5	791			X	X		X			X		X		X	X	
6	21	X				X										
7	22		X		X											
8	23			X	X											
9	31	X		X		X										
10	32		X	X												
11	721	X				X										
12	722		X		X											
13	723				X	X										
14	731	X		X		X										
15	732		X	X												

Último usuario / Última modificación: Ing. Edwin Sotelo Palacios - 20/10/2020 12:02:01

Externo:	3014	Dirección:	KR 24 X CL 55 S	Zona Auto:	3524	Vo.Bo:CMF	ING. CEGZ
Encargado:	Ing. Edwin Sotelo Palacios	Versión:	Implementación_SSI_3014_Versión1.sop6	Fecha:	20/10/2020 15:01:49	Vo.Bo.CPT	
Contrato:	CTO SDM: 20171913	Consortio Movilidad Futura 2050		Sittraffic Office		Vo.Bo.SDM	

Matrices del tiempo intermedio:

N. °	Nombre	Nombre corto	Descripción	MC	CI	Determinación	BDS/SIM	SrIT	DT(SDM)
1	MI_C900V_3014	MI_C900V_3014		MC_C900V_3014	CTI (ZB) 1	Efectiva	Matriz de TINT		











	GS de entrada	1	2	3	4	5	6	7	8	9	10	11	12	13	14	15
GS de despeje		1	2	3	4	791	21	22	23	31	32	721	722	723	731	732
1	1			5	4		4			8		5			8	
2	2		4				4				8		5			8
3	3	4	6	5	4			4	7	10					7	9
4	6	4		5	6		4	8				4	8			
5	791			6	4	4			8		5		6	8		
6	21	7			7											
7	22		10		10											
8	23			13	10											
9	31	4		6	4											
10	32		4	4												
11	721	10			10											
12	722		12		12											
13	723				12	13										
14	731	8		9		8										
15	732		7	6												

Último usuario / Última modificación: Ing. Edwin Sotelo Palacios - 20/10/2020 12:02:01

Externo:	3014	Dirección:	KR 24 X CL 55 S	Zona Auto:	3524	Vo.Bo:CMF	ING. CEGZ
Encargado:	Ing. Edwin Sotelo Palacios	Versión:	Implementación_SSI_3014_Versión1.sop6	Fecha:	20/10/2020 15:01:49	Vo.Bo.CPT	
Contrato:	CTO SDM: 20171913	Consortio Movilidad Futura 2050		Sittraffic Office		Vo.Bo.SDM	

Activar programas \ PC_C900V_3014

Ser. no.	O-Nr.	Nombre	Nombre corto	Descripción	Duración	MTI(ZZ)	MDI	MDF	Subnodo(TK)
1	1	PC_C900V_3014	PC_C900V_3014		18	MI_C900V_3014			

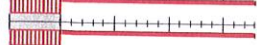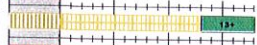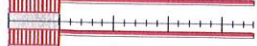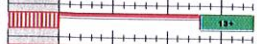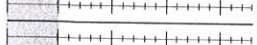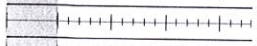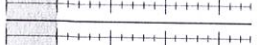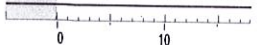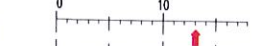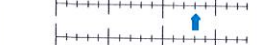Nr	Grupo de señales		W1	W2	W3	W4	W5	W6
1	1		0	13				
2	2		0	13				
3	3		0					
4	6		0					
5	791		0	13				
6	21		0					
7	22		0					
8	23		0	13				
9	31		0					
10	32		0					
11	721							
12	722							
13	723							
14	731							
15	732							

 = Ver  = R  = A  = Ver  = R  = A  = Ver  = R  = A  = Ver  = R  = A

Seguridad de señales	13
Supervisión TI(ZZ)	13
Intervención especial	13

Externo:	3014	Dirección:	KR 24 X CL 55 S	Zona Auto:	3524	Vo.Bo:CMF	ING. CEGZ
Encargado:	Ing. Edwin Sotelo Palacios	Versión:	Implementación_SSI_3014_Versión1.sop6	Fecha:	20/10/2020 15:01:49	Vo.Bo.CPT	
Contrato:	CTO SDM: 20171913	Consortio Movilidad Futura 2050		Sittraffic Office		Vo.Bo.SDM	

Programas de desconexión \ PD_C900V_3014

Ser. no.	O-Nr.	Nombre	Nombre corto	Descripción	Duración	MTI(ZZ)	MDI	MDF	Subnodo(TK)
1	1	PD_C900V_3014	PD_C900V_3014		18	MI_C900V_3014			


Nr	Grupo de señales		W1	W2	W3	W4	W5	W6
1	1		5	18				
2	2		5	18				
3	3		18					
4	6		18					
5	791		5	18				
6	21		18					
7	22		18					
8	23		5	18				
9	31		18					
10	32		18					
11	721							
12	722							
13	723							
14	731							
15	732							

Ver	Osc	Roj	R.In	A.In	A.In
Seguridad de señales					
Supervisión TI(ZZ)					
Intervención especial					

Externo:	3014	Dirección:	KR 24 X CL 55 S	Zona Auto:	3524	Vo.Bo:CMF	ING. CEGZ
Encargado:	Ing. Edwin Sotelo Palacios	Versión:	Implementación_SSI_3014_Versión1.sop6	Fecha:	20/10/2020 15:01:49	Vo.Bo.CPT	
Contrato:	CTO SDM: 20171913	Consorcio Movilidad Futura 2050		Sitraffic Office		Vo.Bo.SDM	


Programas de señal \ PS_1_C900V_3014

Ser. no.	O-Nr.	Nombre corto	Nombre	Descripción	Tiempo de Ciclo	No de Com. Dispo.	Tipo	Desfase	Tabla de volúmenes	MTI(ZZ)	MDI	MDF	COORDINACION	S-Encendido	S-Off	@Point-in-time values based on
1	1	PS_1_C900V_3014	PS_1_C900V_3014		100	1	SG	0		MI_C900V_3014			1	PC_C900V_3014	PD_C900V_3014	0

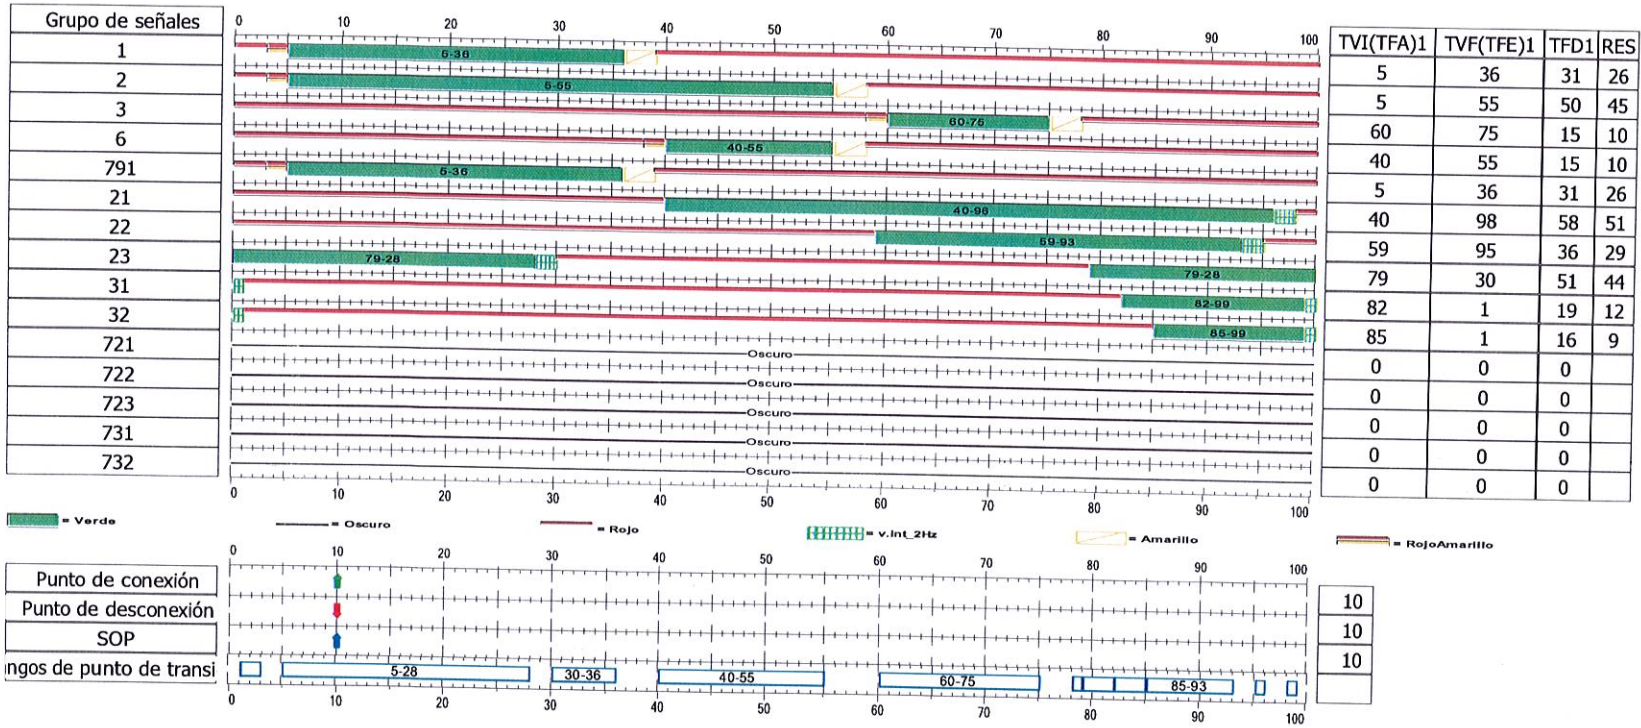


Programas de señal \ PS_2_C900V_3014

Ser. no.	O-Nr.	Nombre corto	Nombre	Descripción	Tiempo de Ciclo	No de Com. Dispo.	Tipo	Desfase	Tabla de volúmenes	MTI(ZZ)	MDI	MDF	COORDINACION	S-Encendido	S-Off	@Point-in-time values based on
2	2	PS_2_C900V_3014	PS_2_C900V_3014		120	2	SG	0		MI_C900V_3014			1	PC_C900V_3014	PD_C900V_3014	0

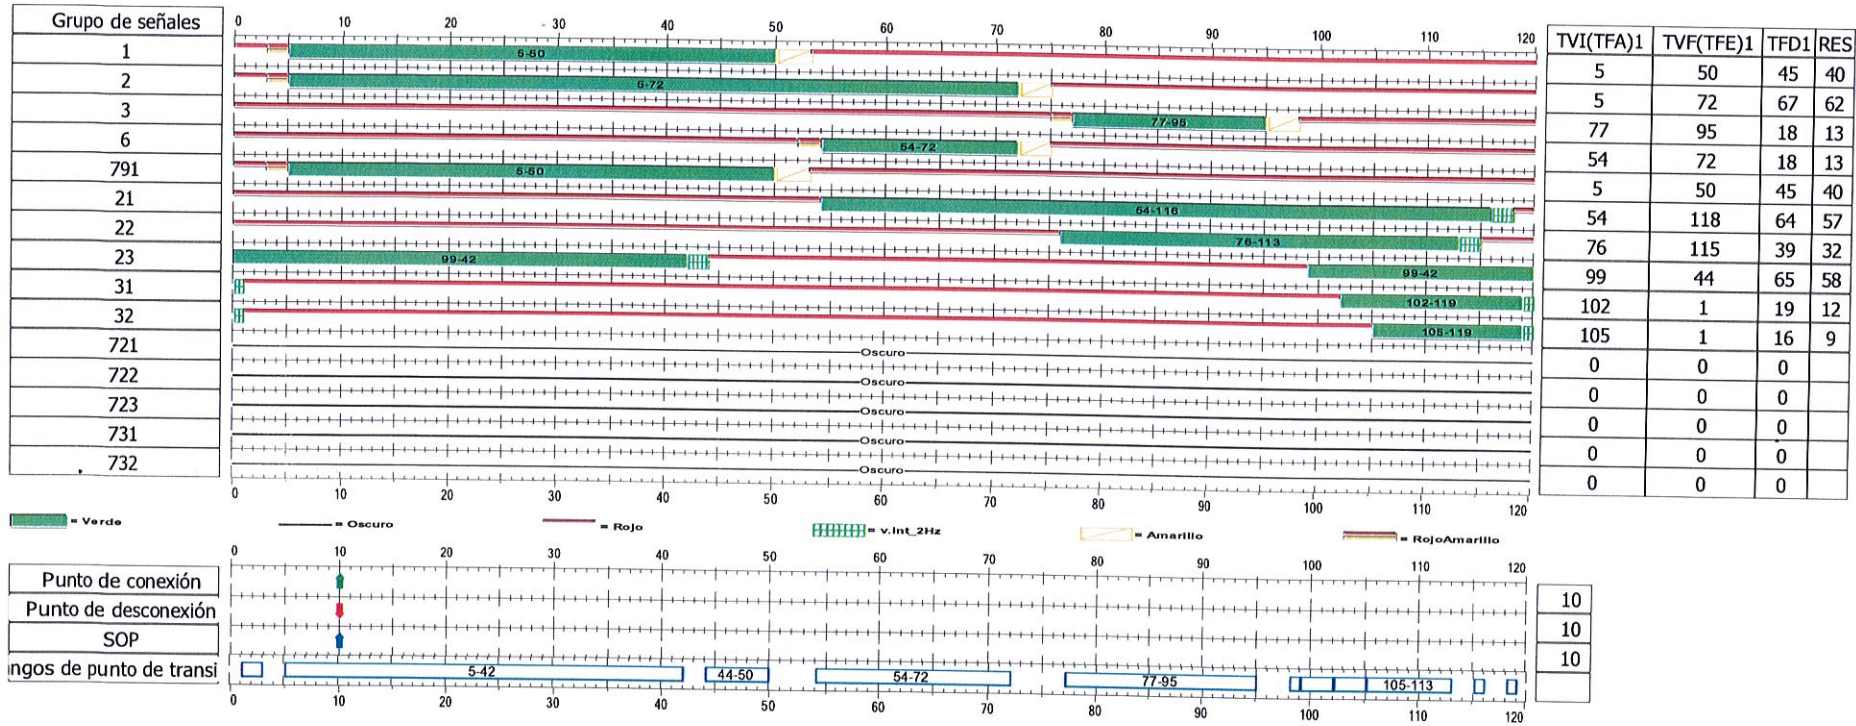

Programas de señal \ PS_3_C900V_3014

Ser. no.	O-Nr.	Nombre corto	Nombre	Descripción	Tiempo de Ciclo	No de Com. Dispo.	Tipo	Desfase	Tabla de volúmenes	MTI(ZZ)	MDI	MDF	COORDINACION	S-Encendido	S-Off	@Point-in-time values based on
3	3	PS_3_C900V_3014	PS_3_C900V_3014		120	3	SG	0		MI_C900V_3014			1	PC_C900V_3014	PD_C900V_3014	0

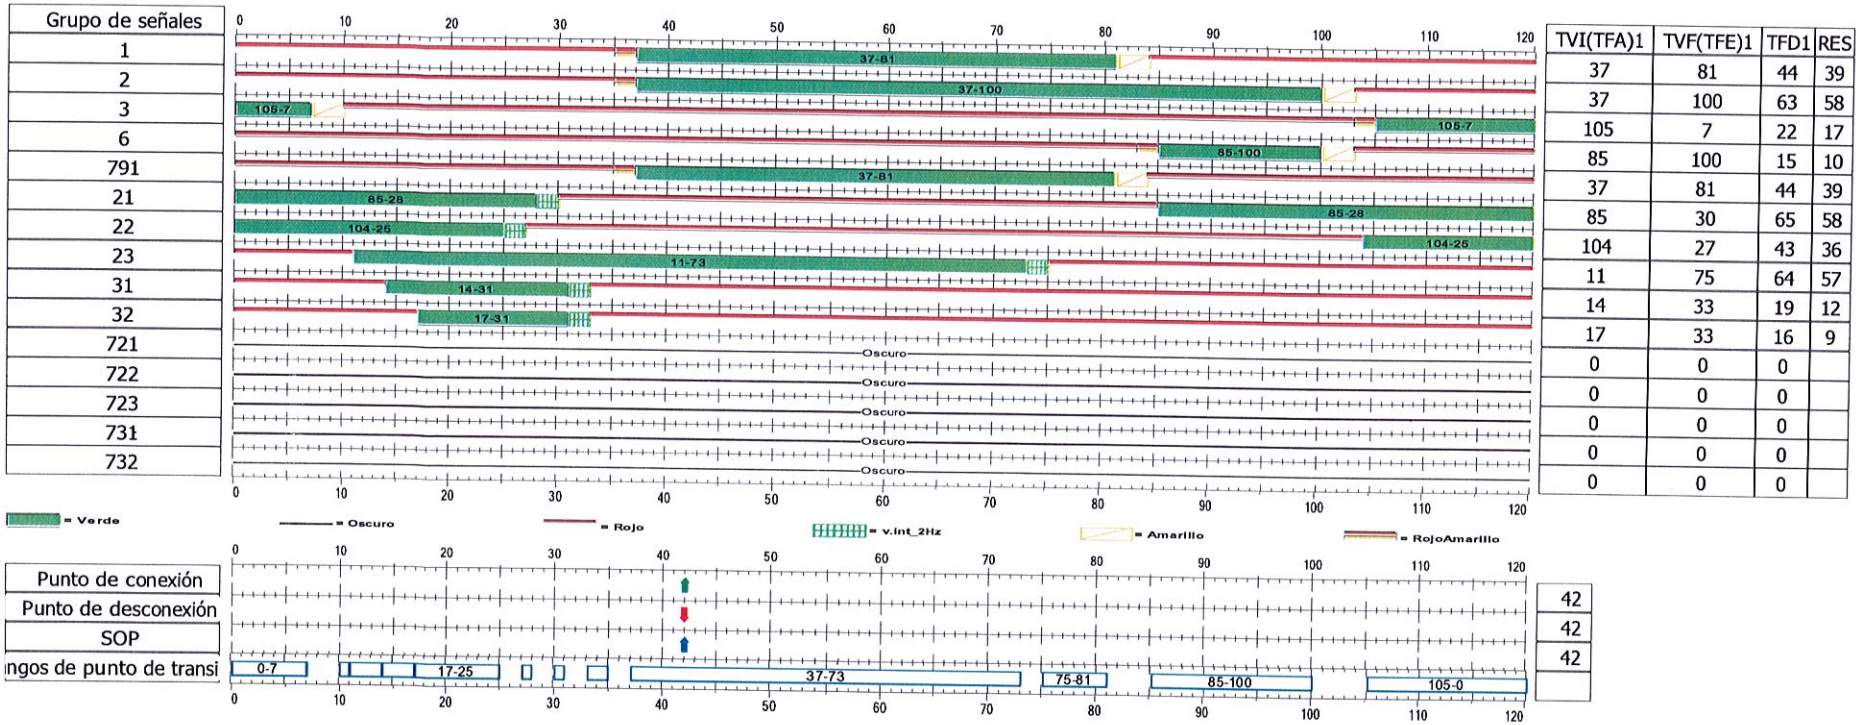


Último usuario / Última actualización = Ing. Edwin Sotelo Palacios / 20/10/2020 1:02:43 p. m.

Externo:	3014	Dirección:	KR 24 X CL 55 S	Zona Auto:	3524	Vo.Bo:CMF	ING. CEG2
Encargado:	Ing. Edwin Sotelo Palacios	Versión:	Implementación_SSI_3014_Versión1.sop6	Fecha:	20/10/2020 15:01:49	Vo.Bo.CPT	
Contrato:	CTO SDM: 20171913	Consortio Movilidad Futura 2050		Sittraffic Office		Vo.Bo.SDM	


Programas de señal \ PS_4_C900V_3014

Ser. no.	O-Nr.	Nombre corto	Nombre	Descripción	Tiempo de Ciclo	No de Com. Dispo.	Tipo	Desfase	Tabla de volúmenes	MTI(ZZ)	MDI	MDF	COORDINACION	S-Encendido	S-Off	@Point-in-time values based on
4	4	PS_4_C900V_3014	PS_4_C900V_3014		120	4	SG	0		MI_C900V_3014			1	PC_C900V_3014	PD_C900V_3014	0

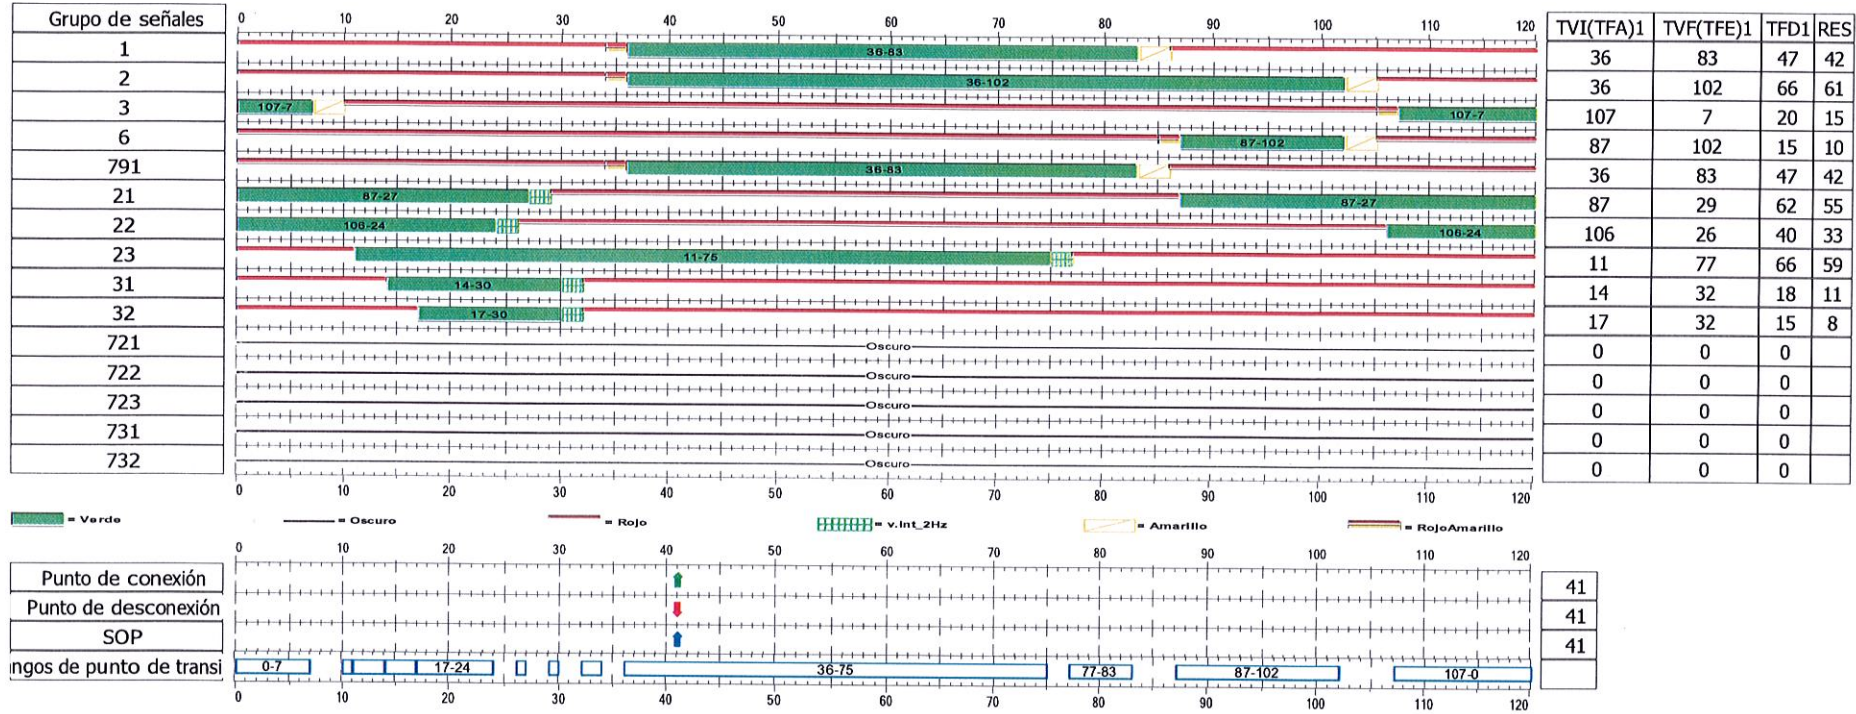

Programas de señal \ PS_5_C900V_3014

Ser. no.	O-Nr.	Nombre corto	Nombre	Descripción	Tiempo de Ciclo	No de Com. Dispo.	Tipo	Desfase	Tabla de volúmenes	MTI(ZZ)	MDI	MDF	COORDINACION	S-Encendido	S-Off	@Point-in-time values based on
5	5	PS_5_C900V_3014	PS_5_C900V_3014		100	5	SG	0		MI_C900V_3014			1	PC_C900V_3014	PD_C900V_3014	0

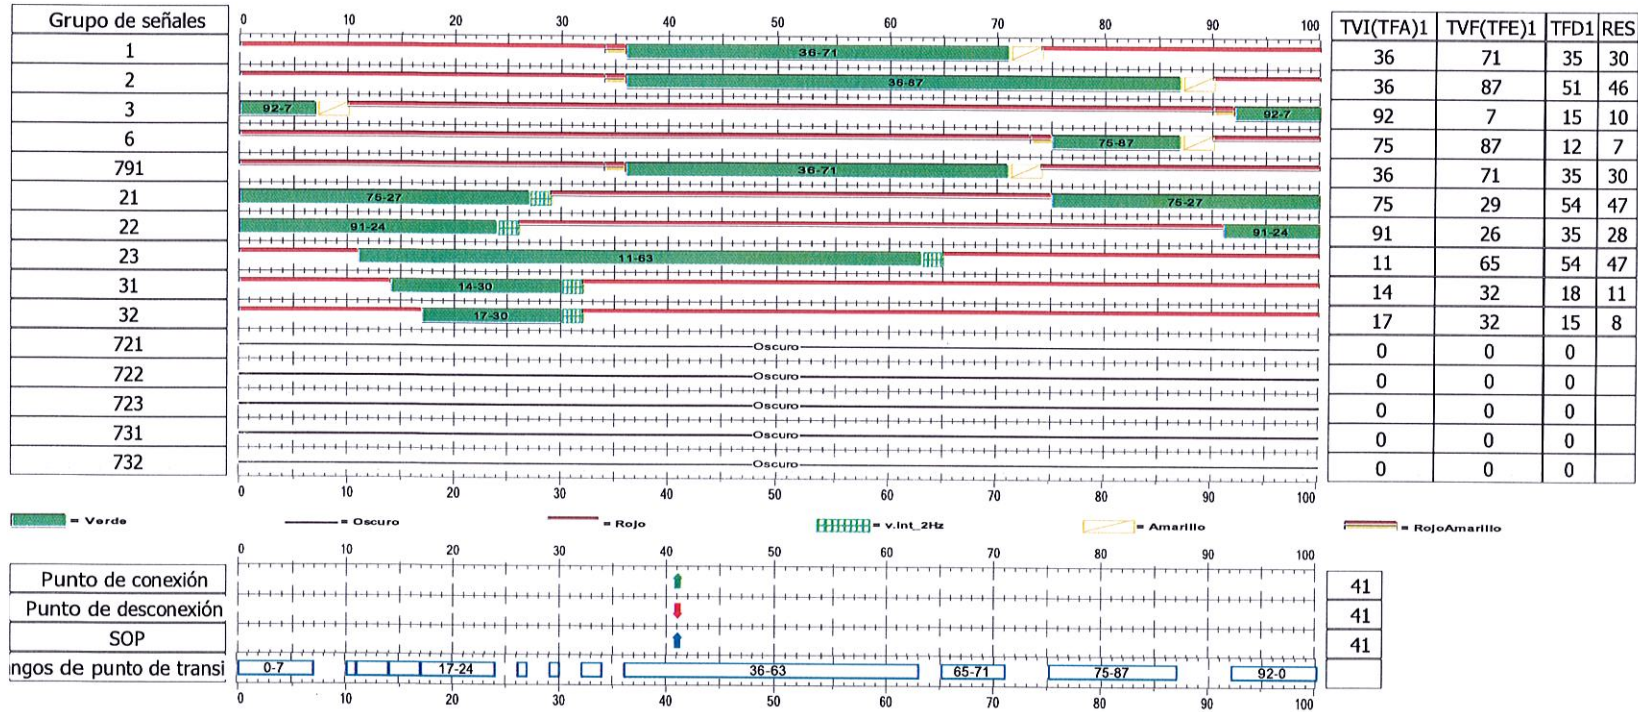


Último usuario / Última actualización = Ing. Edwin Sotelo Palacios / 20/10/2020 2:10:12 p. m.

Externo:	3014	Dirección:	KR 24 X CL 55 S	Zona Auto:	3524	Vo.Bo:CMF	ING. CEG2
Encargado:	Ing. Edwin Sotelo Palacios	Versión:	Implementación_SSI_3014_Versión1.sop6	Fecha:	20/10/2020 15:01:49	Vo.Bo.CPT	
Contrato:	CTO SDM: 20171913	Consortio Movilidad Futura 2050		Sitraffic Office		Vo.Bo.SDM	

Programas de señal \ PS_6_C900V_3014

Ser. no.	O-Nr.	Nombre corto	Nombre	Descripción	Tiempo de Ciclo	No de Com. Dispo.	Tipo	Desfase	Tabla de volúmenes	MTI(ZZ)	MDI	MDF	COORDINACION	S-Encendido	S-Off	@Point-in-time values based on
6	6	PS_6_C900V_3014	PS_6_C900V_3014		100	6	SG	0		MI_C900V_3014			1	PC_C900V_3014	PD_C900V_3014	0

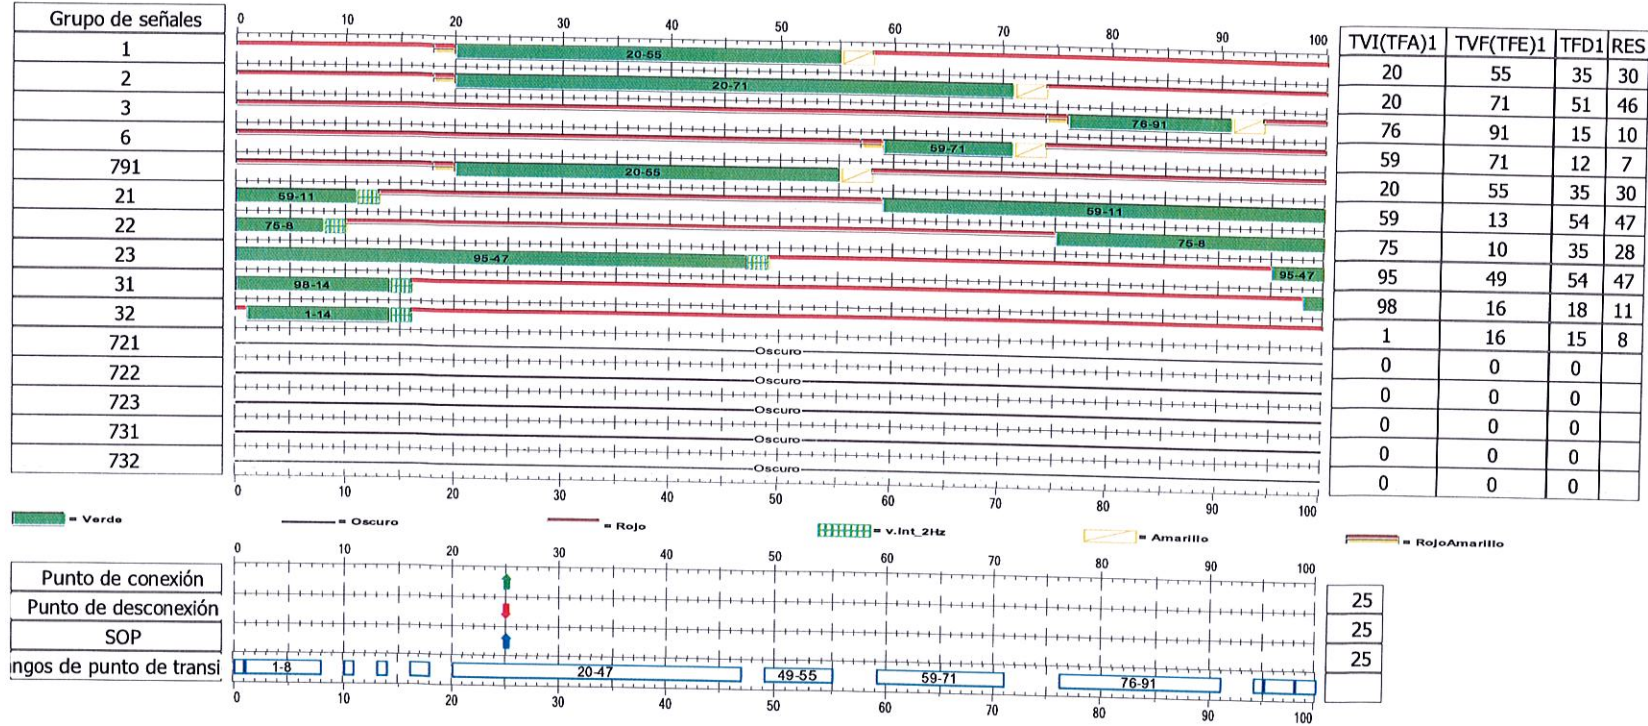


Último usuario / Última actualización = Ing. Edwin Sotelo Palacios / 20/10/2020 2:11:16 p. m.

Externo:	3014	Dirección:	KR 24 X CL 55 S	Zona Auto:	3524	Vo.Bo:CMF	ING. CEG2
Encargado:	Ing. Edwin Sotelo Palacios	Versión:	Implementación_SSI_3014_Versión1.sop6	Fecha:	20/10/2020 15:01:49	Vo.Bo.CPT	
Contrato:	CTO SDM: 20171913	Consortio Movilidad Futura 2050		Sittraffic Office		Vo.Bo.SDM	

Programas de señal \ PS_7_C900V_3014

Ser. no.	O-Nr.	Nombre corto	Nombre	Descripción	Tiempo de Ciclo	No de Com. Dispo.	Tipo	Desfase	Tabla de volúmenes	MTI(ZZ)	MDI	MDF	COORDINACION	S-Encendido	S-Off	@Point-in-time values based on
7	7	PS_7_C900V_3014	PS_7_C900V_3014		90	7	SG	0		MI_C900V_3014			1	PC_C900V_3014	PD_C900V_3014	0

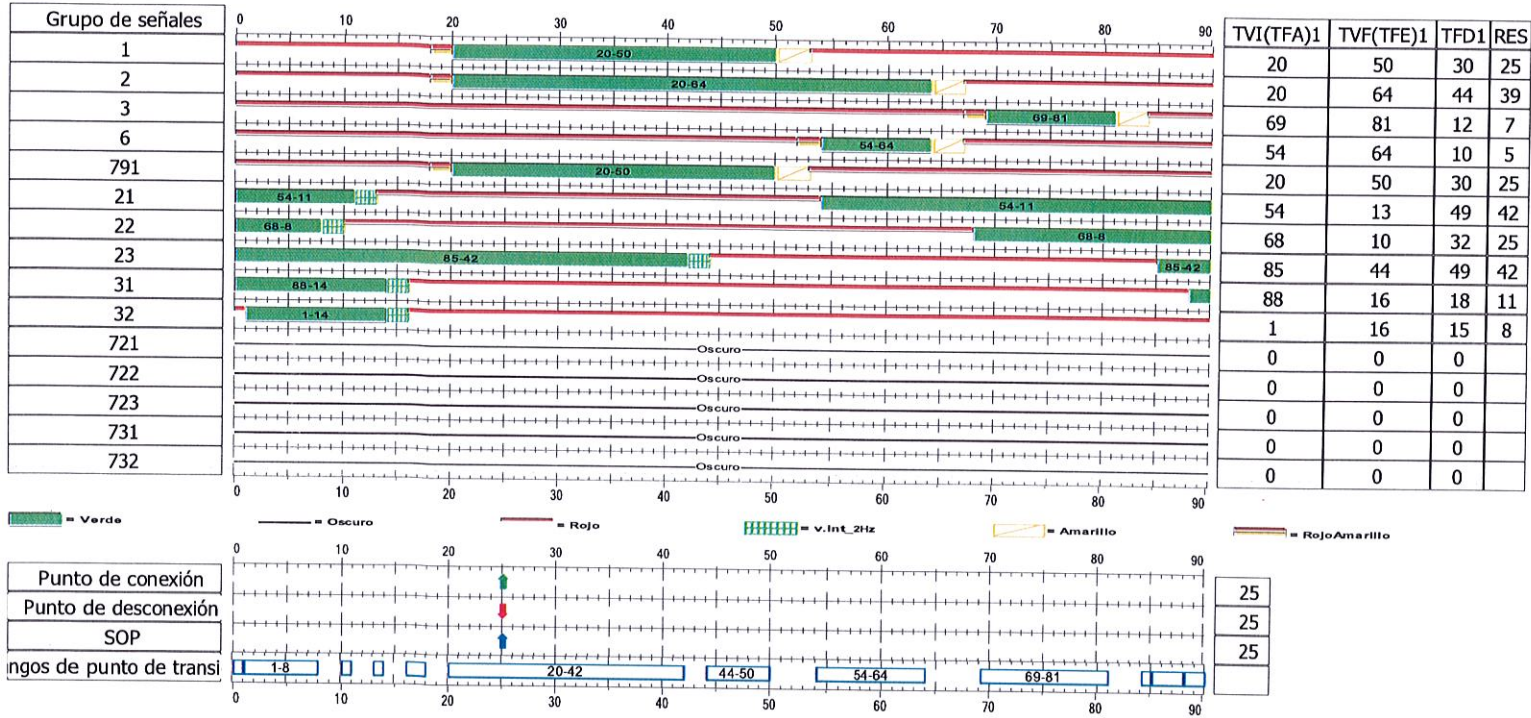


Último usuario / Última actualización = Ing. Edwin Sotelo Palacios / 20/10/2020 2:13:25 p. m.

Externo:	3014	Dirección:	KR 24 X CL 55 S	Zona Auto:	3524	Vo.Bo:CMF	ING. CEG2
Encargado:	Ing. Edwin Sotelo Palacios	Versión:	Implementación_SSI_3014_Versión1.sop6	Fecha:	20/10/2020 15:01:49	Vo.Bo.CPT	
Contrato:	CTO SDM: 20171913	Consortio Movilidad Futura 2050		Sitraffic Office		Vo.Bo.SDM	

Programas de señal \ PS_8_C900V_3014

Ser. no.	O-Nr.	Nombre corto	Nombre	Descripción	Tiempo de Ciclo	No de Com. Dispo.	Tipo	Desfase	Tabla de volúmenes	MTI(ZZ)	MDI	MDF	COORDINACION	S-Encendido	S-Off	@Point-in-time values based on
8	8	PS_8_C900V_3014	PS_8_C900V_3014		75	8	SG	0		MI_C900V_3014			1	PC_C900V_3014	PD_C900V_3014	0

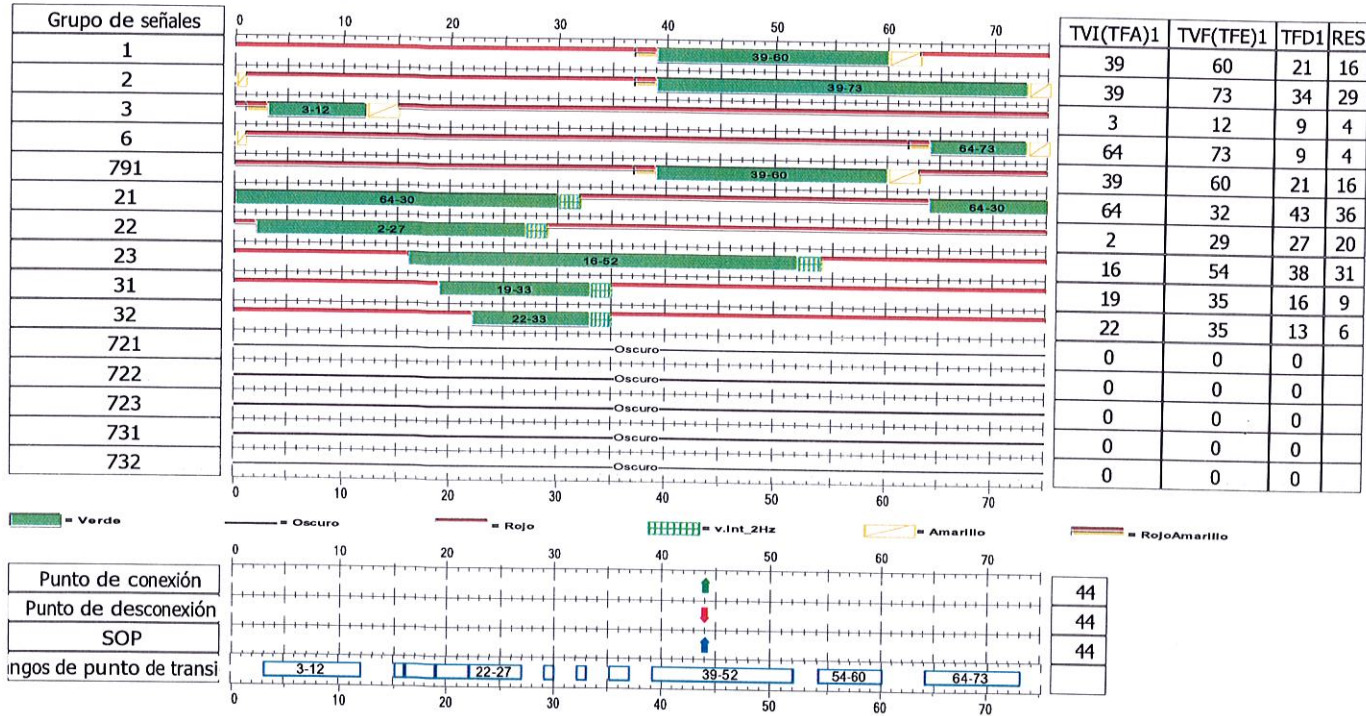


Detectores

No.	Nombre corto	Nombre	Descripción	Tipo de modelo	Distancia Det	Posición	Longitud	Longitud de cola	Cruce	SG	Distancia SL	GL-Alfa1	GL-Alfa2	Umbral	Mexwa Intervalo	Modo	Tipo de conexión
1	B.721.1	B.721.1		Botón				-	721			PREDETERMINADO	PREDETERMINADO	0	60	Estándar	A BORDO
2	B.721.2	B.721.2		Botón				-	721			PREDETERMINADO	PREDETERMINADO	0	60	Estándar	A BORDO
3	B.722.1	B.722.1		Botón				-	722			PREDETERMINADO	PREDETERMINADO	0	60	Estándar	A BORDO
4	B.722.2	B.722.2		Botón				-	722			PREDETERMINADO	PREDETERMINADO	0	60	Estándar	A BORDO
5	B.723.1	B.723.1		Botón				-	722			PREDETERMINADO	PREDETERMINADO	0	60	Estándar	A BORDQ
6	B.723.2	B.723.2		Botón				-	723			PREDETERMINADO	PREDETERMINADO	0	60	Estándar	A BORDO
7	B.731.1	B.731.1		Botón				-	723			PREDETERMINADO	PREDETERMINADO	0	60	Estándar	A BORDO
8	B.731.2	B.731.2		Botón				-	731			PREDETERMINADO	PREDETERMINADO	0	60	Estándar	A BORDO
9	B.732.1	B.732.1		Botón				-	731			PREDETERMINADO	PREDETERMINADO	0	60	Estándar	A BORDO
10	B.732.1	B.732.1		Botón				-	732			PREDETERMINADO	PREDETERMINADO	0	60	Estándar	A BORDO
								-	732			PREDETERMINADO	PREDETERMINADO	0	60	Estándar	A BORDO

No.	Espacio de conexión	Canal de conexión	IndiceExt	ErrorInput	Areas de plausibilidad1	Areas de plausibilidad2	Areas de plausibilidad3	Areas de plausibilidad4
1	0	1		0	Predeterminado	Predeterminado	Predeterminado	Predeterminado
2	0	2		0	Predeterminado	Predeterminado	Predeterminado	Predeterminado
3	0	3		0	Predeterminado	Predeterminado	Predeterminado	Predeterminado
4	0	4		0	Predeterminado	Predeterminado	Predeterminado	Predeterminado
5	0	5		0	Predeterminado	Predeterminado	Predeterminado	Predeterminado
6	0	6		0	Predeterminado	Predeterminado	Predeterminado	Predeterminado
7	0	7		0	Predeterminado	Predeterminado	Predeterminado	Predeterminado
8	0	8		0	Predeterminado	Predeterminado	Predeterminado	Predeterminado
9	0	9		0	Predeterminado	Predeterminado	Predeterminado	Predeterminado
10	0	10		0	Predeterminado	Predeterminado	Predeterminado	Predeterminado

Externo:	3014	Dirección:	KR 24 X CL 55 S	Zona Auto:	3524	Vo.Bo.CMF	ING. CEG2
Encargado:	Ing. Edwin Sotelo Palacios	Versión:	Implementación_SSI_3014_Versión1.sop6	Fecha:	20/10/2020 15:01:49	Vo.Bo.CPT	
Contrato:	CTO SDM: 20171913	Consortio Movilidad Futura 2050		Sittraffic Office		Vo.Bo.SDM	

Definiciones & secuencias de la etapa

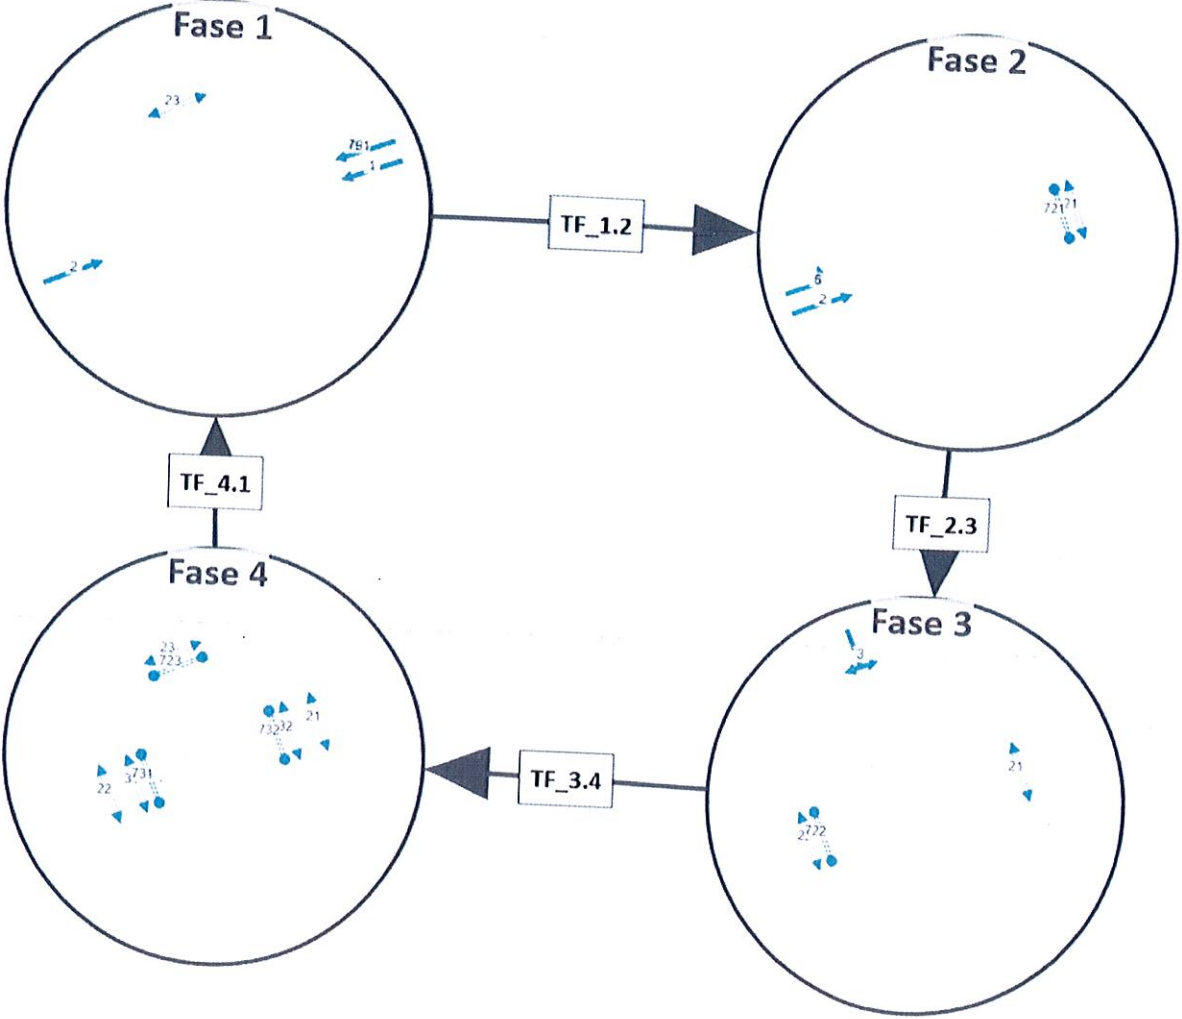

Externo:	3014	Dirección:	KR 24 X CL 55 S	Zona Auto:	3524	Vo.Bo:CMF	ING. CEG2
Encargado:	Ing. Edwin Sotelo Palacios	Versión:	Implementación_SSI_3014_Versión1.sop6	Fecha:	20/10/2020 15:01:49	Vo.Bo.CPT	
Contrato:	CTO SDM: 20171913	Consortio Movilidad Futura 2050		Sittraffic Office		Vo.Bo.SDM	

Bogotá SSI

Secretaría Distrital de Movilidad

TABLA DE CONDICIONES_3014_C900V

EXTERNO 3014

DIRECCION: KR 24 X CL 55 S

Fase	Prioridad	Fase Destino	Condición de Demanda	Condición de Extensión
1	1	2	PD	-
2	1	3	PD	-
3	2	1	PD	-
4	1	1	PD	-


NOTA: Sonoros en función a la detección de los botones.

Externo:	3014	Dirección:	KR 24 X CL 55 S	Zona Auto:	3524	Vo.Bo:CMF	ING. CEGZ
Encargado:	Ing. Edwin Sotelo Palacios	Versión:	Implementación_SSI_3014_Versión1.sop6	Fecha:	20/10/2020 15:01:49	Vo.Bo.CPT	
Contrato:	CTO SDM: 20171913	Consortio Movilidad Futura 2050		Sittraffic Office		Vo.Bo.SDM	

Transiciones de fase \ TF_1.2_C900V_3014

Seq.no.	Nombre	Nombre corto	Descripción	Duración	Desde fase	A fase	O no. BS	O no. TA	Subnodo(TK)	SubTransNr	SubTransVer	MTI(ZZ)	MDI	MDF	Probado	Apagar transito
1	TF_1.2_C900V_3014	TF_1.2	Calculado en la secuencia de fase con las opciones: Conmutac	17	Fase 1	Fase 2		1	1	0	1	MI_C900V_3014				

Seq.no.	SY-/FO-Identificación(EPS)
1	Ninguno

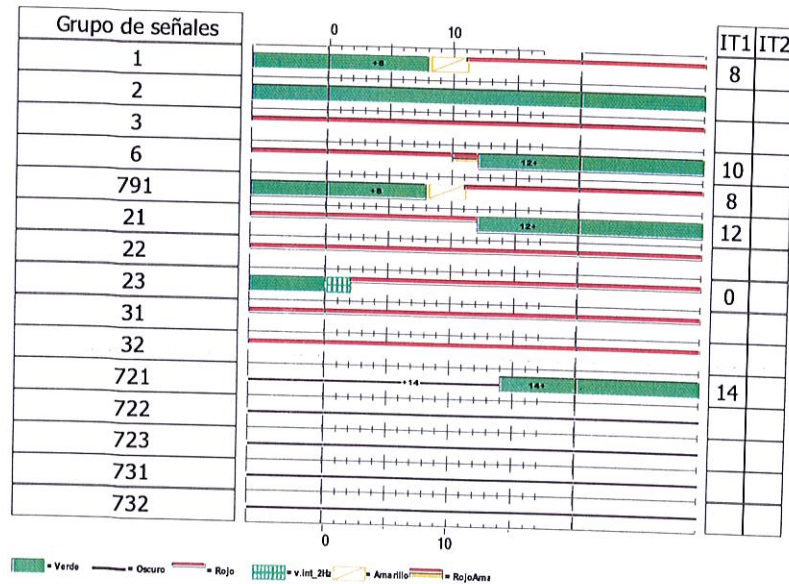


Externo:	3014	Dirección:	KR 24 X CL 55 S				
Encargado:	Ing. Edwin Sotelo Palacios	Versión:	Implementación_SSI_3014_Versión1.sop6	Zona Auto:	3524	Vo.Bo.CMF	ING. CEGZ
Contrato:	CTO SDM: 20171913	Consorcio Movilidad Futura 2050		Fecha:	20/10/2020 15:01:49	Vo.Bo.CPT	
				Sittraffic Office		Vo.Bo.SDM	

Transiciones de fase \ TF_2.3_C900V_3014

Seq.no.	Nombre	Nombre corto	Descripción	Duración	Desde fase	A fase	O no. BS	O no. TA	Subnodo(TK)	SubTransNr	SubTransVer	MTI(ZZ)	MDI	MDF	Probado	Apagar transito
2	TF_2.3_C900V_3014	TF_2.3	Calculado en la secuencia de fase con las opciones: Conmutac	10	Fase 2	Fase 3		2	1	0	1	MI_C900V_3014				

Seq.no.	SY-/FO-Identificación(EPS)
2	Ninguno

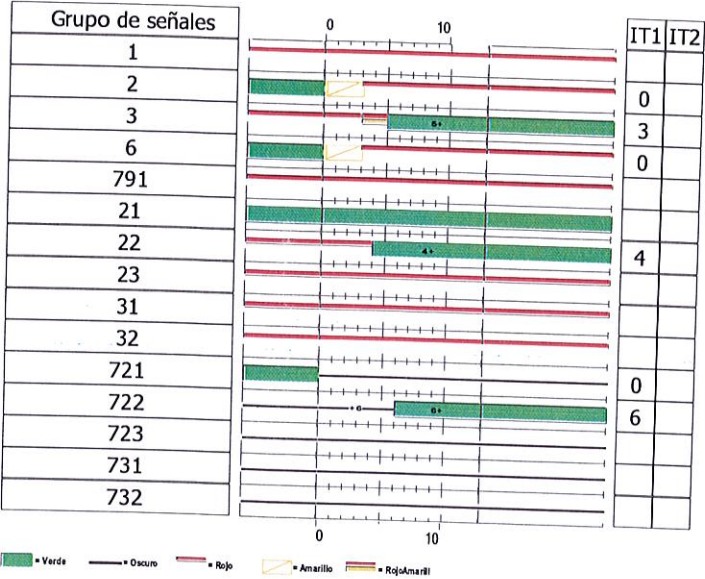


Externo:	3014	Dirección:	KR 24 X CL 55 S	Zona Auto:	3524	Vo.Bo:CMF	ING. CEGZ
Encargado:	Ing. Edwin Sotelo Palacios	Versión:	Implementación_SSI_3014_Versión1.sop6	Fecha:	20/10/2020 15:01:49	Vo.Bo.CPT	
Contrato:	CTO SDM: 20171913	Consortio Movilidad Futura 2050		Sittraffic Office		Vo.Bo.SDM	

Transiciones de fase \ TF_3.4_C900V_3014

Seq.no.	Nombre	Nombre corto	Descripción	Duración	Desde fase	A fase	O no. BS	O no. TA	Subnodo(TK)	SubTransNr	SubTransVer	MTI(ZZ)	MDI	MDF	Probado	Apagar transito
3	TF_3.4_C900V_3014	TF_3.4	Calculado en la secuencia de fase con las opciones: Conmutac	15	Fase 3	Fase 4		3	1	0	1	MI_C900V_3014				


Seq.no.	SY-/FO-Identificación(EPS)
3	Ninguno

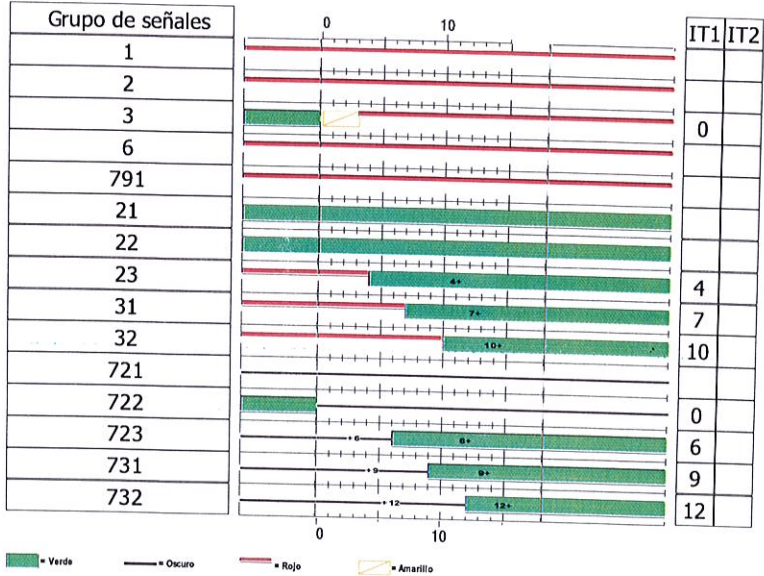

Externo:	3014	Dirección:	KR 24 X CL 55 S	Zona Auto:	3524	Vo.Bo:CMF	ING. CEG2
Encargado:	Ing. Edwin Sotelo Palacios	Versión:	Implementación_SSI_3014_Versión1.sop6	Fecha:	20/10/2020 15:01:49	Vo.Bo.CPT	
Contrato:	CTO SDM: 20171913	Consortio Movilidad Futura 2050		Sittraffic Office		Vo.Bo.SDM	

Transiciones de fase \ TF_4.1_C900V_3014


Seq.no.	SY-/FO-Identificación(EPS)
4	Ninguno

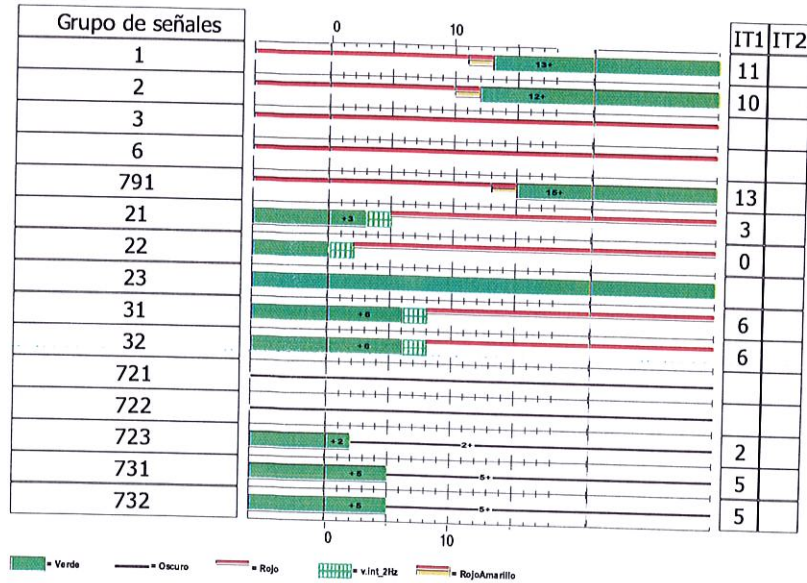

Externo:	3014	Dirección:	KR 24 X CL 55 S				
Encargado:	Ing. Edwin Sotelo Palacios	Versión:	Implementación_SSI_3014_Versión1.sop6	Zona Auto:	3524	Vo.Bó:CMF	ING. CEGZ
Contrato:	CTO SDM: 20171913	Consortio Movilidad Futura 2050		Fecha:	20/10/2020 15:01:49	Vo.Bó.CPT	
				Sittraffic Office		Vo.Bó.SDM	

Planes de permisividad de fase \ PP_1_C900V_3014


Ser. no.	O-Nr.	Nombre	Nombre corto	Descripción	Programa de señal	Tiempo de Ciclo	Punto de conexión	Punto de desconexión	SOP	Plan de secuencia de fases	Segundo inicial
1	1	PP_1_C900V_3014	PP_1_C900V_3014		PS_1_C900V_3014	100	10	10	10		0

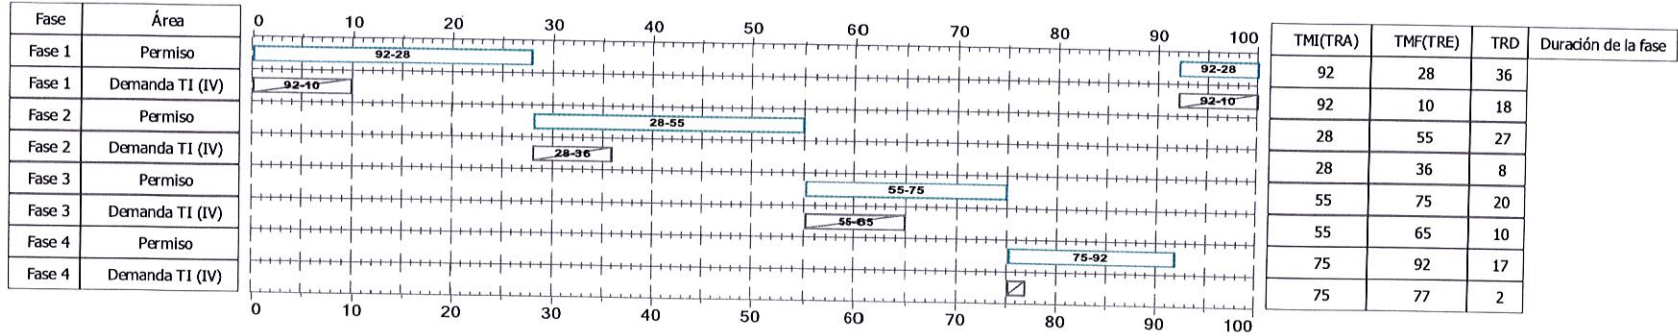

Externo:	3014	Dirección:	KR 24 X CL 55 S	Zona Auto:	3524	Vo.Bo:CMF	ING. CEGZ
Encargado:	Ing. Edwin Sotelo Palacios	Versión:	Implementación_SSI_3014_Versión1.sop6	Fecha:	20/10/2020 15:01:49	Vo.Bo.CPT	
Contrato:	CTO SDM: 20171913	Consortio Movilidad Futura 2050		Sittraffic Office		Vo.Bo.SDM	

Planes de permisividad de fase \ PP_2_C900V_3014


Ser. no.	O-Nr.	Nombre	Nombre corto	Descripción	Programa de señal	Tiempo de Ciclo	Punto de conexión	Punto de desconexión	SOP	Plan de secuencia de fases	Segundo inicial
2	2	PP_2_C900V_3014	PP_2_C900V_3014		PS_2_C900V_3014	120	10	10	10		0

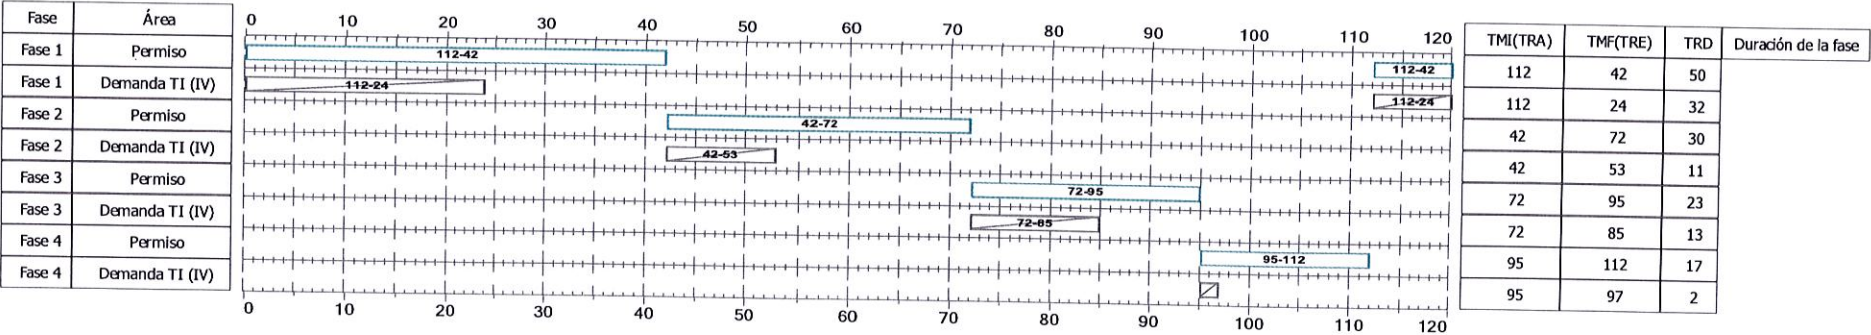

Externo:	3014	Dirección:	KR 24 X CL 55 S	Zona Auto:	3524	Vo.Bo:CMF	ING. CEGZ
Encargado:	Ing. Edwin Sotelo Palacios	Versión:	Implementación_SSI_3014_Versión1.sop6	Fecha:	20/10/2020 15:01:49	Vo.Bo.CPT	
Contrato:	CTO SDM: 20171913	Consortio Movilidad Futura 2050		Sittraffic Office		Vo.Bo.SDM	

Planes de permisividad de fase \ PP_3_C900V_3014


Ser. no.	O-Nr.	Nombre	Nombre corto	Descripción	Programa de señal	Tiempo de Ciclo	Punto de conexión	Punto de desconexión	SOP	Plan de secuencia de fases	Segundo inicial
3	3	PP_3_C900V_3014	PP_3_C900V_3014		PS_3_C900V_3014	120	42	42	42		0

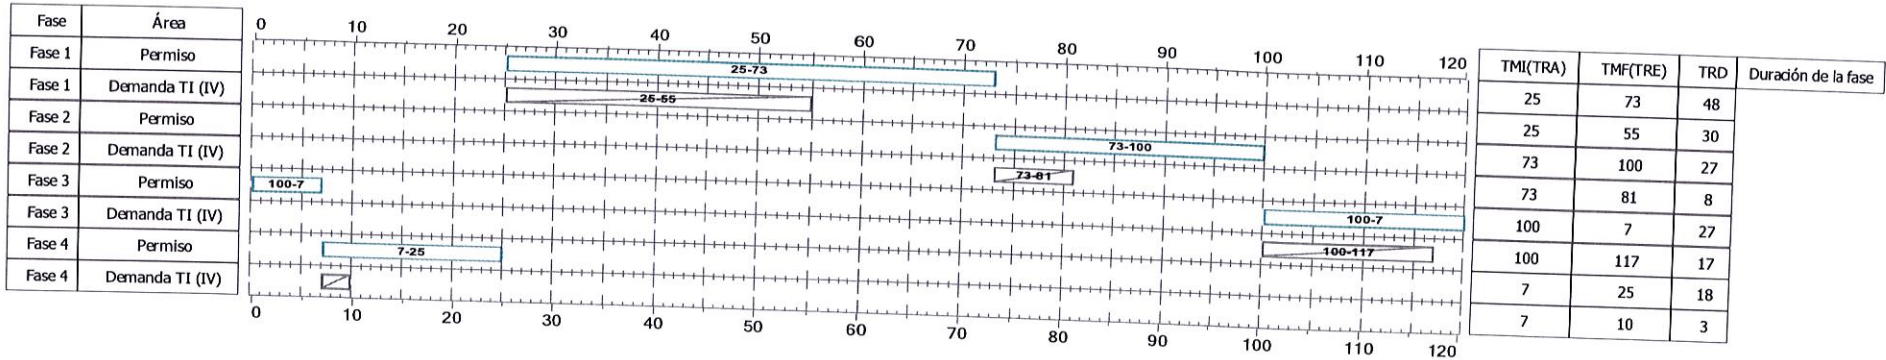

Externo:	3014	Dirección:	KR 24 X CL 55 S	Zona Auto:	3524	Vo.Bo:CMF	ING. CEGZ
Encargado:	Ing. Edwin Sotelo Palacios	Versión:	Implementación_SSI_3014_Versión1.sop6	Fecha:	20/10/2020 15:01:49	Vo.Bo.CPT	
Contrato:	CTO SDM: 20171913	Consortio Movilidad Futura 2050		Sittraffic Office		Vo.Bo.SDM	

Planes de permisividad de fase \ PP_4_C900V_3014


Ser. no.	O-Nr.	Nombre	Nombre corto	Descripción	Programa de señal	Tiempo de Ciclo	Punto de conexión	Punto de desconexión	SOP	Plan de secuencia de fases	Segundo inicial
4	4	PP_4_C900V_3014	PP_4_C900V_3014		PS_4_C900V_3014	120	41	41	41		0

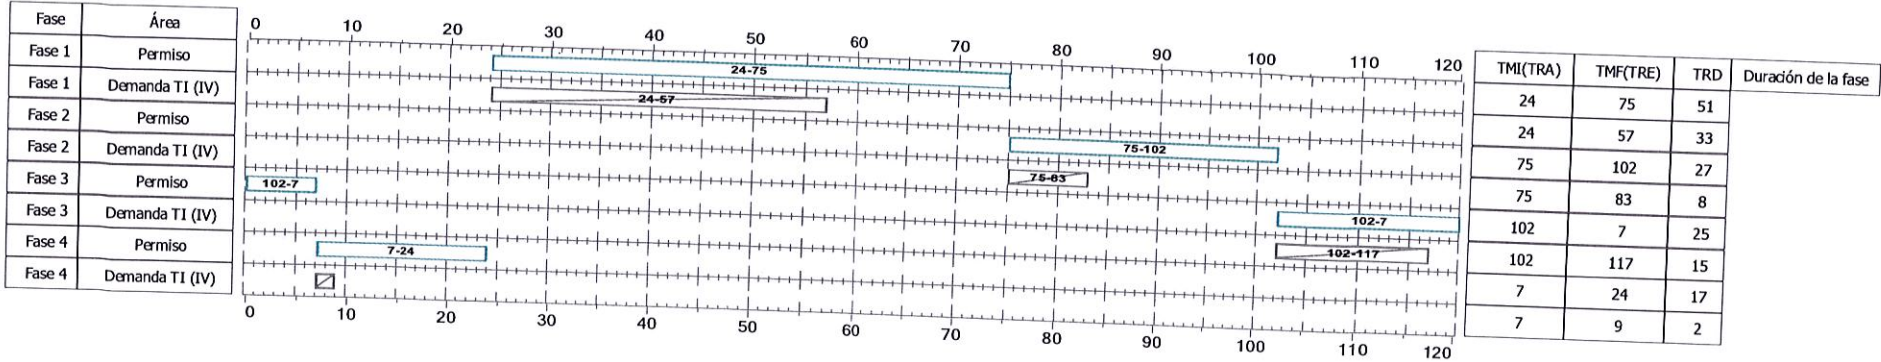

Externo:	3014	Dirección:	KR 24 X CL 55 S	Zona Auto:	3524	Vo.Bo:CMF	ING. CEG2
Encargado:	Ing. Edwin Sotelo Palacios	Versión:	Implementación_SSI_3014_Versión1.sop6	Fecha:	20/10/2020 15:01:49	Vo.Bo.CPT	
Contrato:	CTO SDM: 20171913	Consortio Movilidad Futura 2050		Sittraffic Office		Vo.Bo.SDM	

Planes de permisividad de fase \ PP_5_C900V_3014


Ser. no.	O-Nr.	Nombre	Nombre corto	Descripción	Programa de señal	Tiempo de Ciclo	Punto de conexión	Punto de desconexión	SOP	Plan de secuencia de fases	Segundo inicial
5	5	PP_5_C900V_3014	PP_5_C900V_3014		PS_5_C900V_3014	100	41	41	41		0

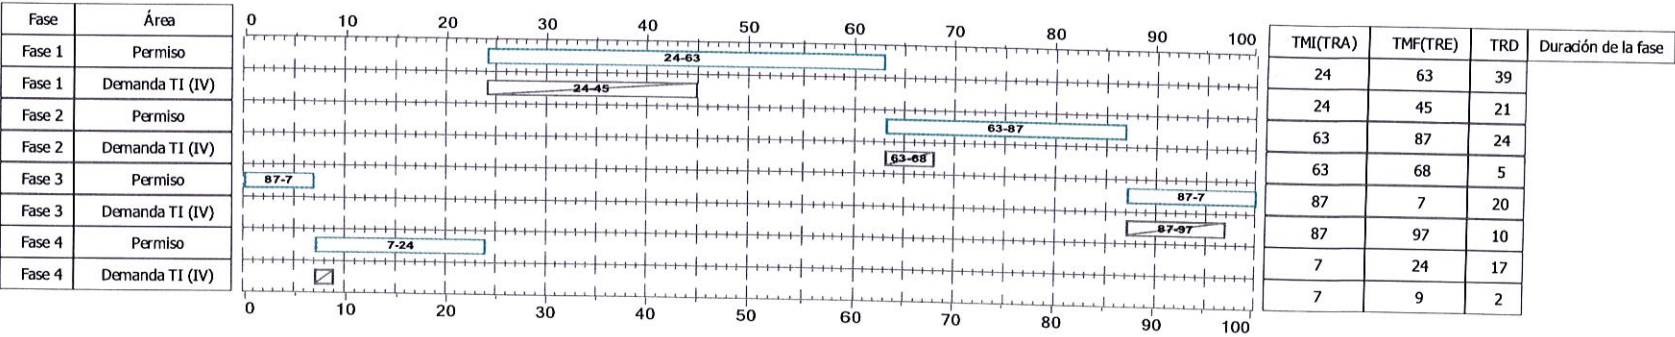

Externo:	3014	Dirección:	KR 24 X CL 55 S	Zona Auto:	3524	Vo.Bo:CMF	ING. CEGZ
Encargado:	Ing. Edwin Sotelo Palacios	Versión:	Implementación_SSI_3014_Versión1.sop6	Fecha:	20/10/2020 15:01:49	Vo.Bo.CPT	
Contrato:	CTO SDM: 20171913	Consortio Movilidad Futura 2050		Sitraffic Office		Vo.Bo.SDM	

Planes de permisividad de fase \ PP_6_C900V_3014


Ser. no.	O-Nr.	Nombre	Nombre corto	Descripción	Programa de señal	Tiempo de Ciclo	Punto de conexión	Punto de desconexión	SOP	Plan de secuencia de fases	Segundo inicial
6	6	PP_6_C900V_3014	PP_6_C900V_3014		PS_6_C900V_3014	100	25	25	25		0

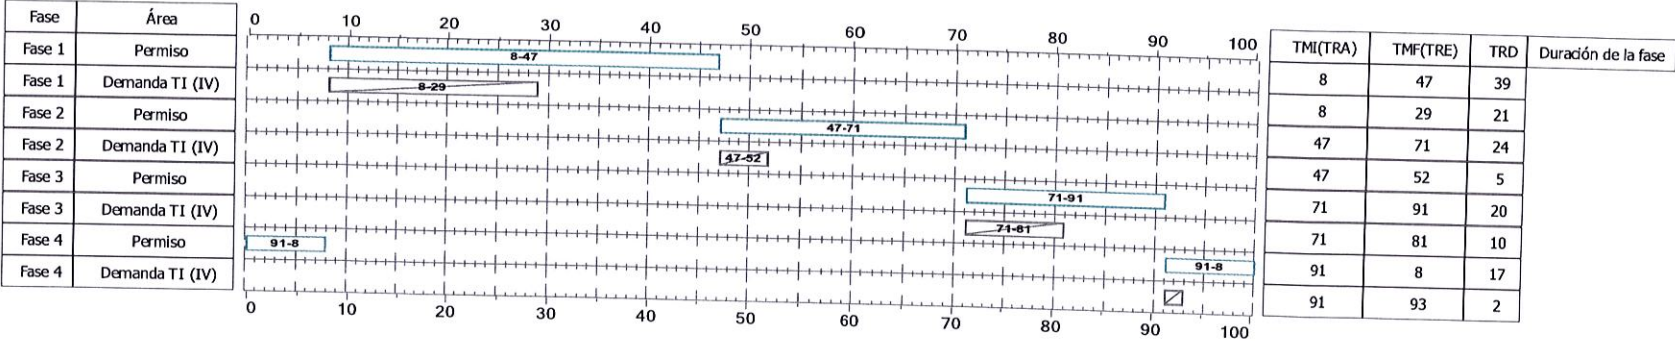

Externo:	3014	Dirección:	KR 24 X CL 55 S	Zona Auto:	3524	Vo.Bo:CMF	ING. CEGZ
Encargado:	Ing. Edwin Sotelo Palacios	Versión:	Implementación_SSI_3014_Versión1.sop6	Fecha:	20/10/2020 15:01:49	Vo.Bo.CPT	
Contrato:	CTO SDM: 20171913	Consortio Movilidad Futura 2050		Sittraffic Office		Vo.Bo.SDM	

Planes de permisividad de fase \ PP_7_C900V_3014


Ser. no.	O-Nr.	Nombre	Nombre corto	Descripción	Programa de señal	Tiempo de Ciclo	Punto de conexión	Punto de desconexión	SOP	Plan de secuencia de fases	Segundo inicial
7	7	PP_7_C900V_3014	PP_7_C900V_3014		PS_7_C900V_3014	90	25	25	25		0

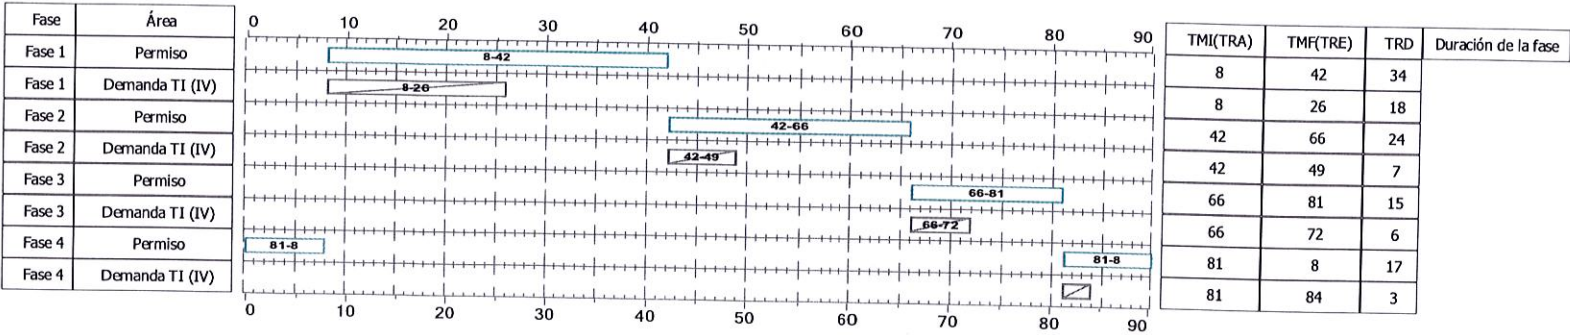

Externo:	3014	Dirección:	KR 24 X CL 55 S	Zona Auto:	3524	Vo.Bo:CMF	ING. CEG2
Encargado:	Ing. Edwin Sotelo Palacios	Versión:	Implementación_SSI_3014_Versión1.sop6	Fecha:	20/10/2020 15:01:49	Vo.Bo.CPT	
Contrato:	CTO SDM: 20171913	Consortio Movilidad Futura 2050		Sittraffic Office		Vo.Bo.SDM	

Planes de permisividad de fase \ PP_8_C900V_3014

Ser. no.	O-Nr.	Nombre	Nombre corto	Descripción	Programa de señal	Tiempo de Ciclo	Punto de conexión	Punto de desconexión	SOP	Plan de secuencia de fases	Segundo inicial
8	8	PP_8_C900V_3014	PP_8_C900V_3014		PS_8_C900V_3014	75	44	44	44	SPS 1	0

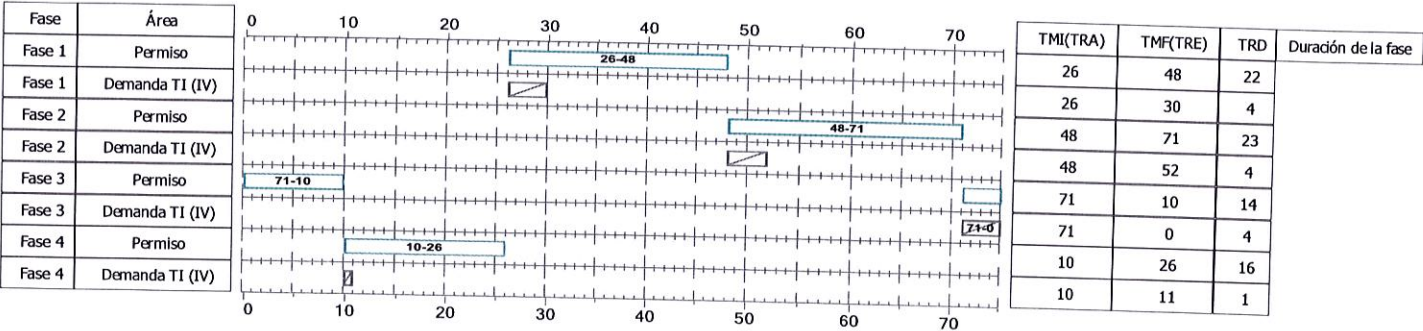

Externo:	3014	Dirección:	KR 24 X CL 55 S	Zona Auto:	3524	Vo.Bo:CMF	ING. CEGZ
Encargado:	Ing. Edwin Sotelo Palacios	Versión:	Implementación_SSI_3014_Versión1.sop6	Fecha:	20/10/2020 15:01:49	Vo.Bo.CPT	
Contrato:	CTO SDM: 20171913	Consortio Movilidad Futura 2050		Sittraffic Office		Vo.Bo.SDM	

PROTOCOLO DE PRUEBA_PS_1_C900V

