

	SISTEMA INTEGRADO DE GESTIÓN DISTRITAL BAJO EL ESTÁNDAR MIPG	
	PROCESO DE INGENIERÍA DE TRÁNSITO	
	ACTA DE ENTREGA - PLANEAMIENTO SEMAFÓRICO	
	Código: PM03-PR07-F06	Versión: 2.0

ACTA DE ENTREGA - PLANEAMIENTO SEMAFÓRICO

DATOS GENERALES		COMUNICACIONES		FUNCIONAMIENTO	GRUPOS	MODIFICACIONES
NÚMERO EXTERNO:	3693	CONEXIÓN:	CENTRAL	Activación de sonoro		Inicio PMT
EQUIPO:	C900	PROTOCOLO:	OCIT2.0	Brechas		
ZONA PLANEAMIENTO:	SUR	FUNCIONAMIENTO	R-TF	Fases por demanda vehicular		
ZONA AUTOMÁTICA:	3605	TIPO DE PROGRAMACIÓN LÓGICA	N.A.	Fases por demanda peatonal		
				Fases por demanda peatonal sonoro		



DIRECCIÓN	FASES	DISPOSITIVOS	ESTADO DISPOSITIVOS	GRUPOS COMPLEMENTO			
ID SIG: 985	AK 14 X CL 13A S	2	- -	-	-	-	

CANTIDADES MODIFICADAS:		Cant.		Cant.		Cant.	
Esquema	1	Tabla Detectores		Archivo Digital Planeamiento	1	SEMA_3693_VersiónPMT.sop6	
Automático Interno (AI)	1	Parámetros TA		Archivo Digital de Simulación			
Matriz de conflictos (MC)		Parámetros CA		Protocolo de Prueba PS			
Matriz de Tiempos Intermedios (MI)	1	Tabla de Condiciones / Diagrama de Flujo					
Plan de Conexión (PC)	1	Plan Secuencia de Fases (SF)					
Plan de Desconexión (PD)	1	Transiciones de Fase (TF)					
Planes de Señales (PS)	13/13	Planes de Permisividad (PP)					

OBSERVACIONES:
Se entrega Planeamiento por Inicio de PMT AK 14. Se realiza cierre de un carril de salida del grupo 2B de acuerdo a esquema.

PROCESO	NOMBRE Y CARGO	FIRMA	FECHA
Elaboró	Ing. Alexandra Pataquiva O. Contratista SDM		20/11/2025
Aprobó :	Profesional Especializado SDM		26/11/2025

CONVENCIONES:	Modo Local:	TF: Tiempos Fijos - TA: Trafico Actuado	NOTA:	* Para programación SL, los parametros se encuentran en la SF.
	Modo Central:	CA: Central Adaptativa - R: Responsivo - RP: Responsivo Pasivo - BT: Basado Tiempo		* Los cambios se resaltan en color gris

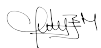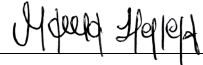OPERACIONES	
Operaciones _ Contrato de Mantenimiento	Operaciones SDM
Diego A Rodriguez	29-dic-2025 
Operador	Fecha Implementación:
	29/12/2025 Manuela Herrera



SISTEMA INTEGRADO DE GESTIÓN DISTRITAL BAJO EL ESTÁNDAR MIPG

PROCESO DE INGENIERÍA DE TRÁNSITO

PROGRAMACIÓN AUTOMÁTICO INTERNO

Código: PM03-PR07-F04

Versión: 3.0

DATOS GENERALES

NÚMERO EXTERNO:

EQUIPO:

3693

C900

ID SIG:

985

DIRECCIÓN

AK 14 X CL 13A S

ZONA AUTOMATICA			
3605			
ASIGNACIÓN DÍA DE LA SEMANA AL PLAN DIARIO			
DÍA DE LA SEMANA	AUTOMÁTICO DE SEMANA (TP)	TP1	
Lunes a Jueves	1	HORA	MINUTO
Viernes	4	PLAN	
Sábado	2		
Domingo / Festivo	3		

TP1		
HORA	MINUTO	PLAN
4	00	7
4	30	6
5	00	2
8	00	3
10	00	9
11	00	3
12	30	9
13	30	3
15	00	4
16	30	3
17	00	4
21	30	3
22	00	7
23	00	8

TP4		
HORA	MINUTO	PLAN
4	00	7
4	30	6
5	00	2
8	00	3
10	00	9
11	00	3
13	30	9
15	00	4
16	30	3
17	00	4
21	30	7
23	00	8

TP2		
HORA	MINUTO	PLAN
4	30	7
5	00	6
5	30	2
10	00	3
13	00	4
14	00	9
15	00	3
16	30	4
18	30	3
20	00	4
22	00	7
23	30	8

TP3		
HORA	MINUTO	PLAN
5	00	6
6	00	2
7	00	5
10	00	10
12	00	5
14	00	3
16	30	4
18	00	3
20	00	7
23	30	8

OBSERVACIONES:



Se entrega Al actualizando los TP1 y TP3 de acuerdo a Automático de Semana.

PROCESO	NOMBRE Y CARGO	FIRMA	FECHA
Elaboró:	Ing. Alexandra Pataquiva O. Contratista SDM		20/11/2025
Aprobó:	Profesional Especializado SDM		26/11/2025


CONVENCIONES

TP: Automático de semana

NOTA: * Los cambios se resaltan en color gris ☐

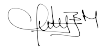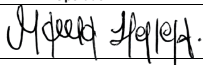OPERACIONES	
Operaciones _ Contrato de Mantenimiento	Operaciones SDM
	29-dic-2025 
Operador	Fecha Implementación:
	29/12/2025 Manuela Herrera

Esquema

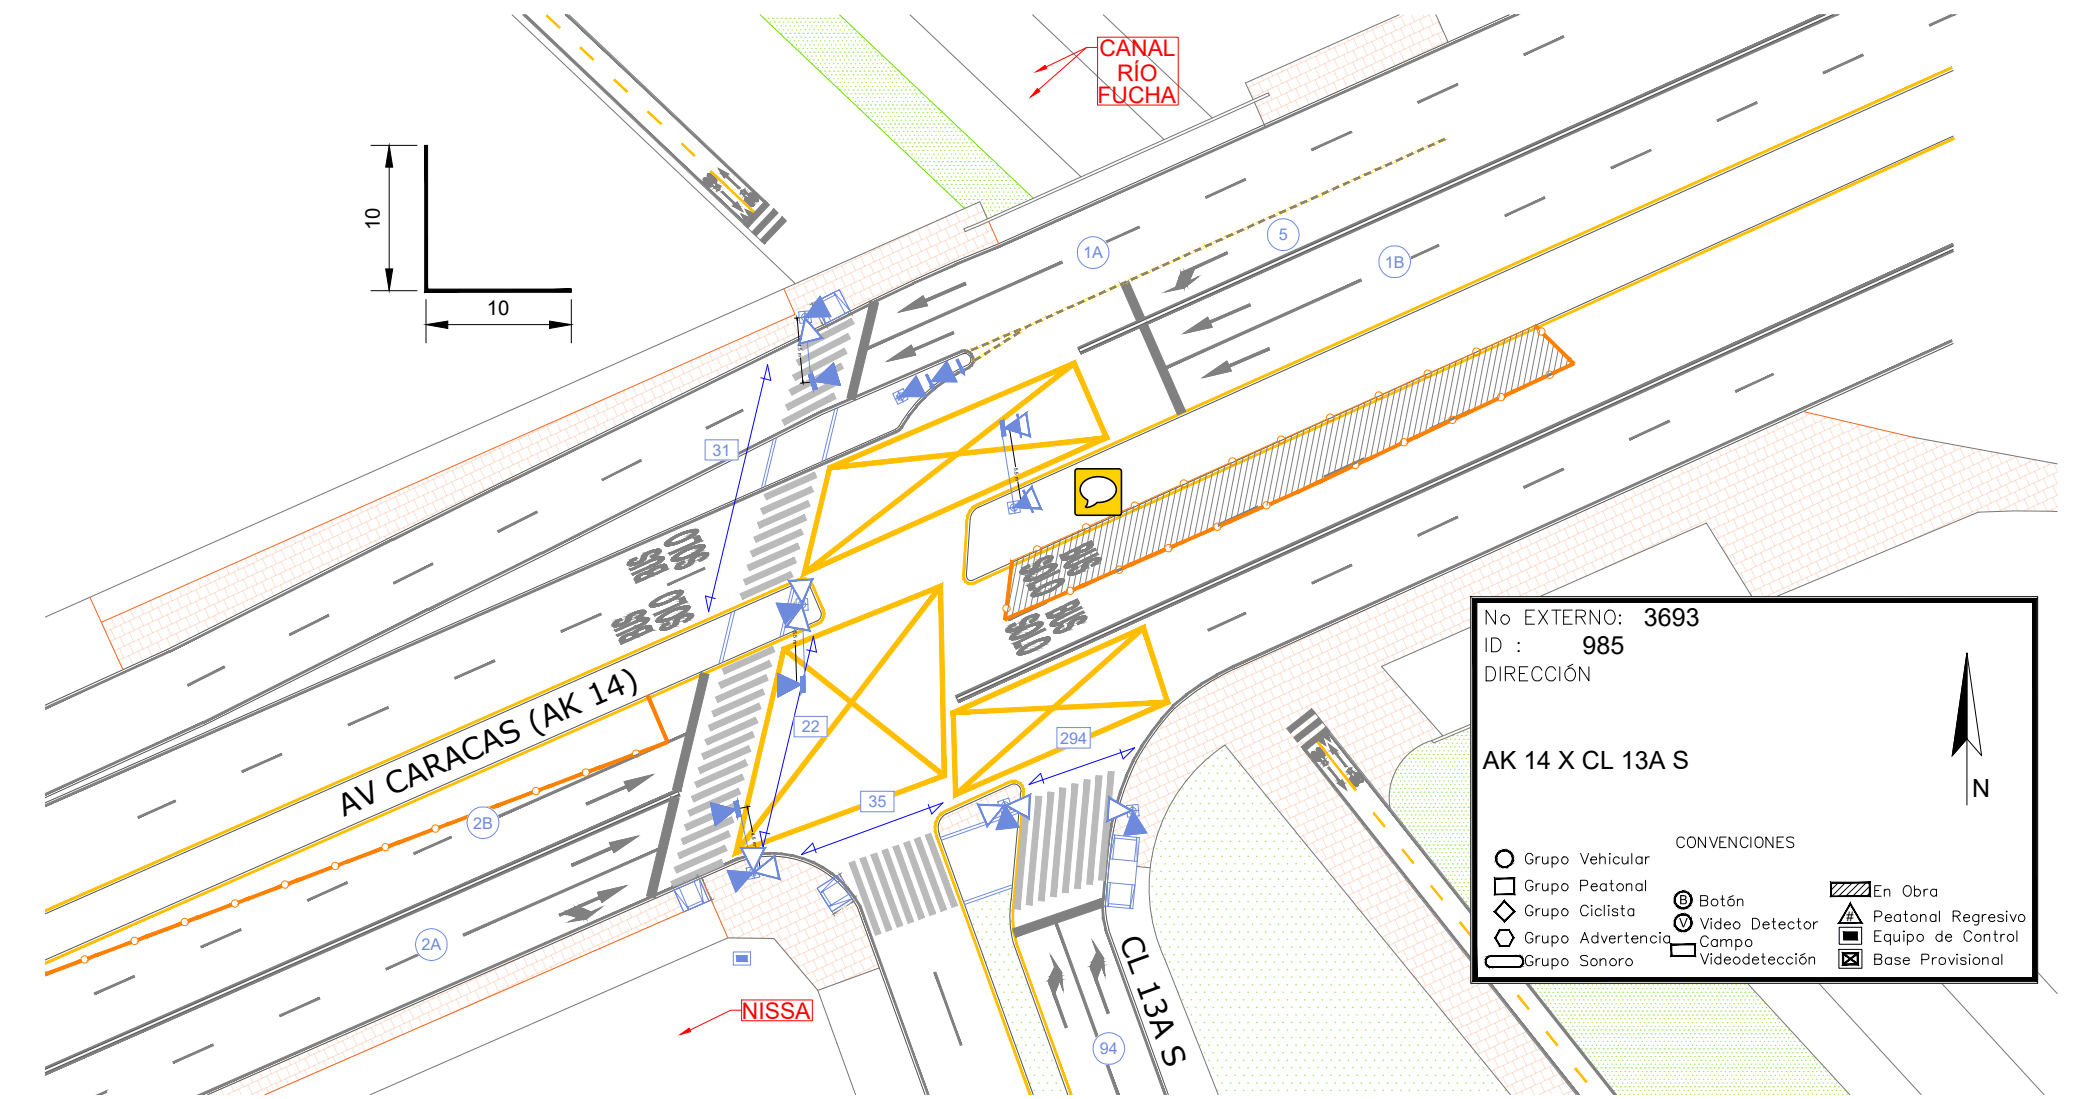

Externo:	3693	Dirección:	AK 14 X CL 13A S	Zona Auto.:	3605
Encargado:	Ing. Alexandra Pataquiva O.	Versión:	SEMA_3693_VersiónPMT.sop6	Fecha:	20/11/2025 17:26:56
Contrato:	2025 - 380	SDM - Subdirección de Semaforización		Sitraffic Office	

Referencias del grupo de señales

Matrices de conflicto:

N.º	Nombre	Nombre corto	Descripción
1	MC_C900_3693	MC_C900_3693	

	GS de entrada											
		1	2	3	4	5	6	7	8	9	10	
GS de despeje		1A	1B	2A	2B	5	94	22	294	31	35	
1	1A									x		
2	1B					x				x		
3	2A					x	x	x				
4	2B					x		x				
5	5		x	x	x						x	
6	94			x					x			
7	22			x	x							
8	294						x					
9	31	x	x									
10	35					x						

Último usuario / Última modificación: Ing. Alexandra Pataquiva O - 20/11/2025 15:37:54

Verificado por / el:

Externo:	3693	Dirección:	AK 14 X CL 13A S	Zona Auto.:	3605
Encargado:	Ing. Alexandra Pataquiva O.	Versión:	SEMA_3693_VersiónPMT.sop6	Fecha:	20/11/2025 17:40:33
Contrato:	2025 - 380	SDM - Subdirección de Semaforización		Sitraffic Office	

Matrices del tiempo intermedio:

N.º	Nombre	Nombre corto	Descripción	MC	CI	Determinación	BDS/SIM	SrT	DT(SDM)
1	MI_C900_3693	MI_C900_3693		MC_C900_3693	CTI (ZB) 1	Efectiva	Matriz de TINT 1	1	1

	GS de entrada													
		1A	1B	2A	2B	5	94	22	294	31	35			
1	1A									5				
2	1B					8				11				
3	2A					4	6	5						
4	2B					7		9						
5	5		5	8	8						11			
6	94			4					4					
7	22			16	16									
8	294						7							
9	31	19	17											
10	35					4								



Último usuario / Última modificación: Ing. Alexandra Pataquiva O - 20/11/2025 15:38:26

Verificado por / el:

Externo:	3693	Dirección:	AK 14 X CL 13A S	Zona Auto.:	3605
Encargado:	Ing. Alexandra Pataquiva O.	Versión:	SEMA_3693_VersiónPMT.sop6	Fecha:	20/11/2025 17:40:33
Contrato:	2025 - 380	SDM - Subdirección de Semaforización			Sitraffic Office

Activar programas \ PC_C900_3693



Ser. no.	O-Nr.	Nombre	Nombre corto	Descripción	Duración	MTI(ZZ)	MDI	MDF	Subnodo(TK)
1	1	PC_C900_3693	PC_C900_3693		24	MI_C900_3693			

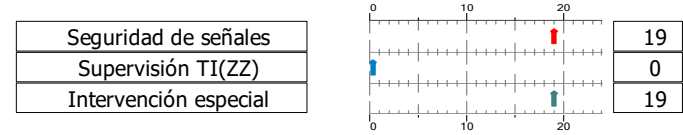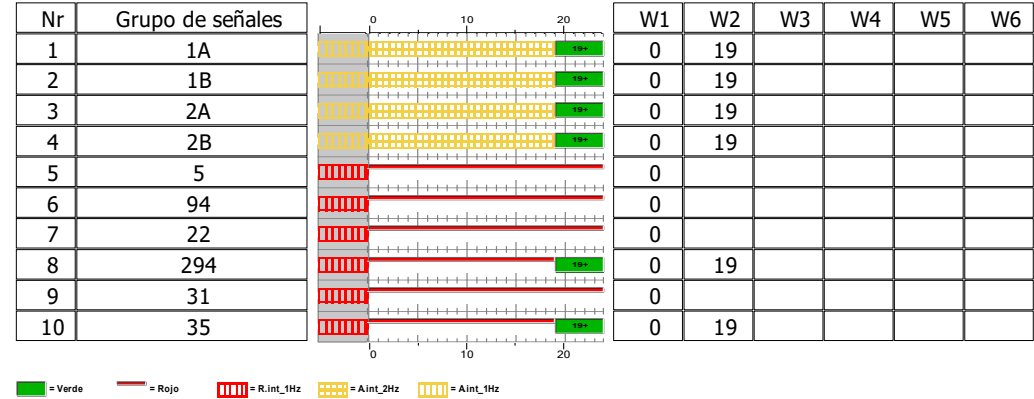

Externo:	3693	Dirección:	AK 14 X CL 13A S	Zona Auto.:	3605
Encargado:	Ing. Alexandra Pataquiva O.	Versión:	SEMA_3693_VersiónPMT.sop6	Fecha:	20/11/2025 17:40:33
Contrato:	2025 - 380	SDM - Subdirección de Semaforización		Sittraffic Office	

Programas de desconexión \ PD_C900_3693


Ser. no.	O-Nr.	Nombre	Nombre corto	Descripción	Duración	MTI(ZZ)	MDI	MDF	Subnodo(TK)
1	1	PD_C900_3693	PD_C900_3693		24	MI_C900_3693			

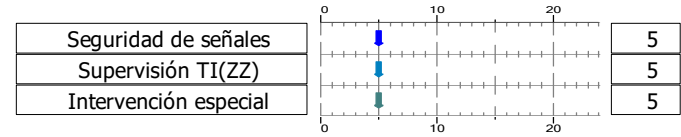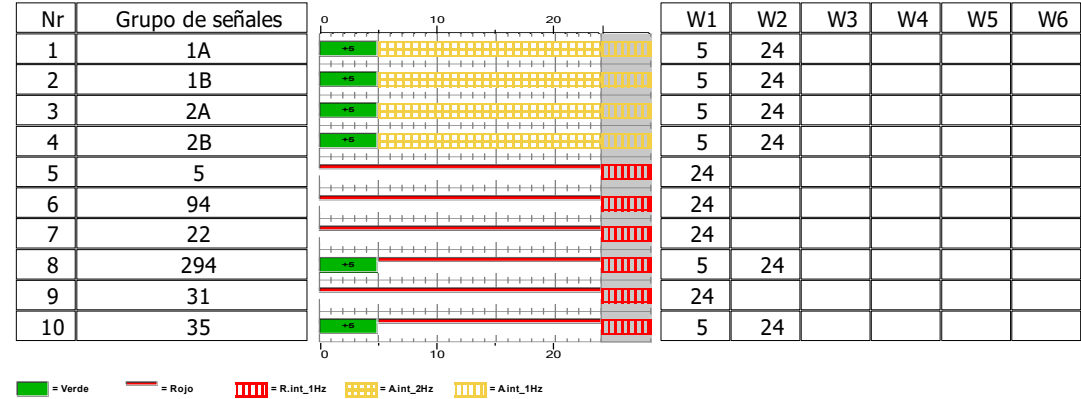

Externo:	3693	Dirección:	AK 14 X CL 13A S	Zona Auto.:	3605
Encargado:	Ing. Alexandra Pataquiva O.	Versión:	SEMA_3693_VersiónPMT.sop6	Fecha:	20/11/2025 17:40:33
Contrato:	2025 - 380	SDM - Subdirección de Semaforización		Sittraffic Office	

Programas de señal \ PS_1_C900_3693

Ser. no.	O-Nr.	Nombre corto	Nombre	Descripción	Tiempo de Ciclo	No de Com. Dispo.	Tipo	Desfase	Tabla de volúmenes	MTI(ZZ)	MDI	MDF	COORDINACION	S-Encendido	S-Off	@Point-in-time values based on
1	1	PS_1_C900_3693	PS_1_C900_3693		100	1	SG	0		MI_C900_3693			1	PC_C900_3693	PD_C900_3693	0

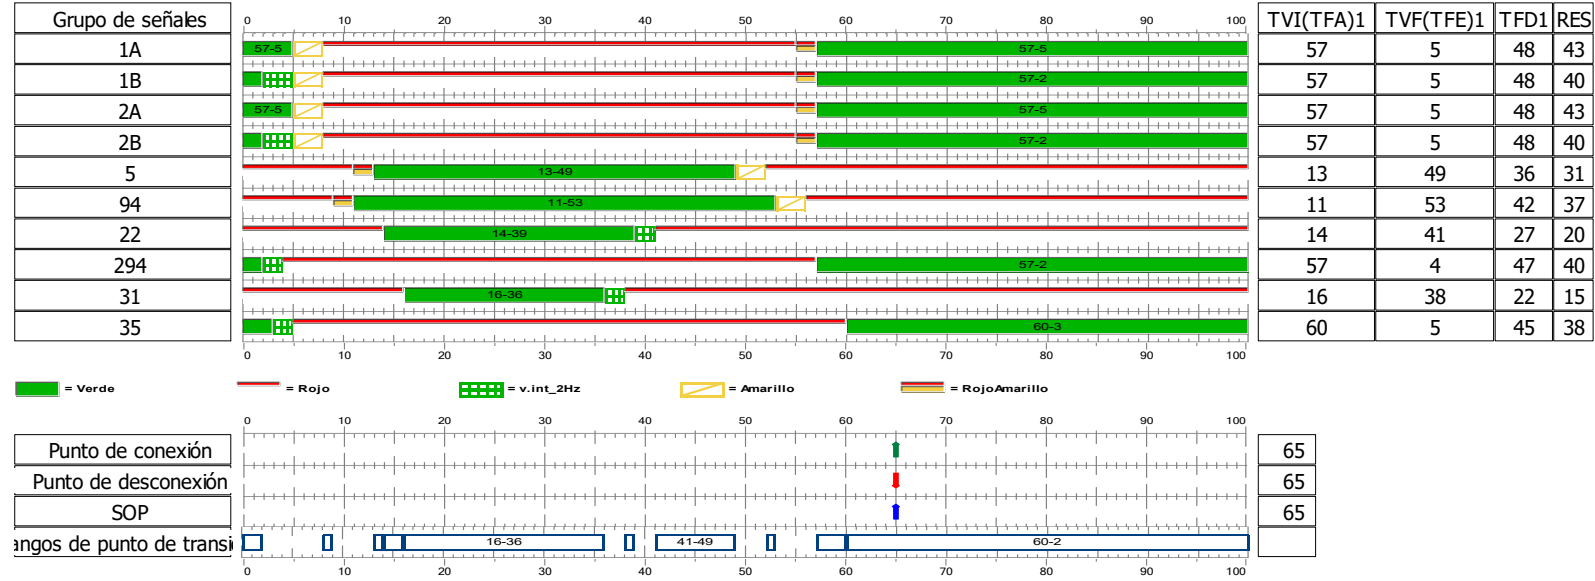


Último usuario / Última actualización = Ing. Alexandra Pataquiva O / 20/11/2025 15:40:48

Externo:	3693	Dirección:	AK 14 X CL 13A S	Zona Auto.:	3605
Encargado:	Ing. Alexandra Pataquiva O.	Versión:	SEMA_3693_VersiónPMT.sop6	Fecha:	20/11/2025 17:40:33
Contrato:	2025 - 380	SDM - Subdirección de Semaforización		Sitraffic Office	

Programas de señal \ PS_2_C900_3693

Ser. no.	O-Nr.	Nombre corto	Nombre	Descripción	Tiempo de Ciclo	No de Com. Dispo.	Tipo	Desfase	Tabla de volúmenes	MT(ZZ)	MDI	MDF	COORDINACION	S-Encendido	S-Off	@Point-in-time values based on
2	2	PS_2_C900_3693	PS_2_C900_3693		100	2	SG	0		MI_C900_3693			1	PC_C900_3693	PD_C900_3693	0

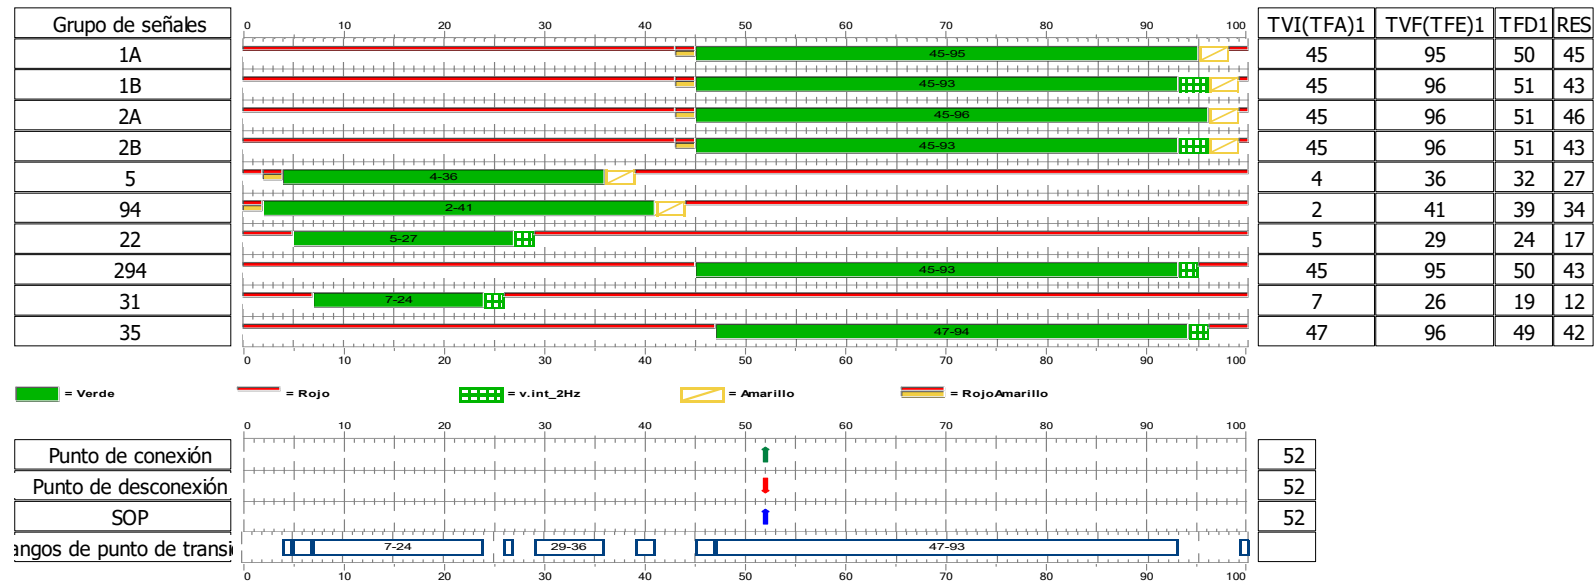


Último usuario / Última actualización = Ing. Alexandra Pataquiva O / 20/11/2025 15:41:28

Externo:	3693	Dirección:	AK 14 X CL 13A S	Zona Auto.:	3605
Encargado:	Ing. Alexandra Pataquiva O.	Versión:	SEMA_3693_VersiónPMT.sop6	Fecha:	20/11/2025 17:40:33
Contrato:	2025 - 380	SDM - Subdirección de Semaforización		Sittraffic Office	

Programas de señal \ PS_3_C900_3693

Ser. no.	O-Nr.	Nombre corto	Nombre	Descripción	Tiempo de Ciclo	No de Com. Dispo.	Tipo	Desfase	Tabla de volúmenes	MT(ZZ)	MDI	MDF	COORDINACION	S-Encendido	S-Off	@Point-in-time values based on
3	3	PS_3_C900_3693	PS_3_C900_3693		100	3	SG	0		MI_C900_3693			1	PC_C900_3693	PD_C900_3693	0

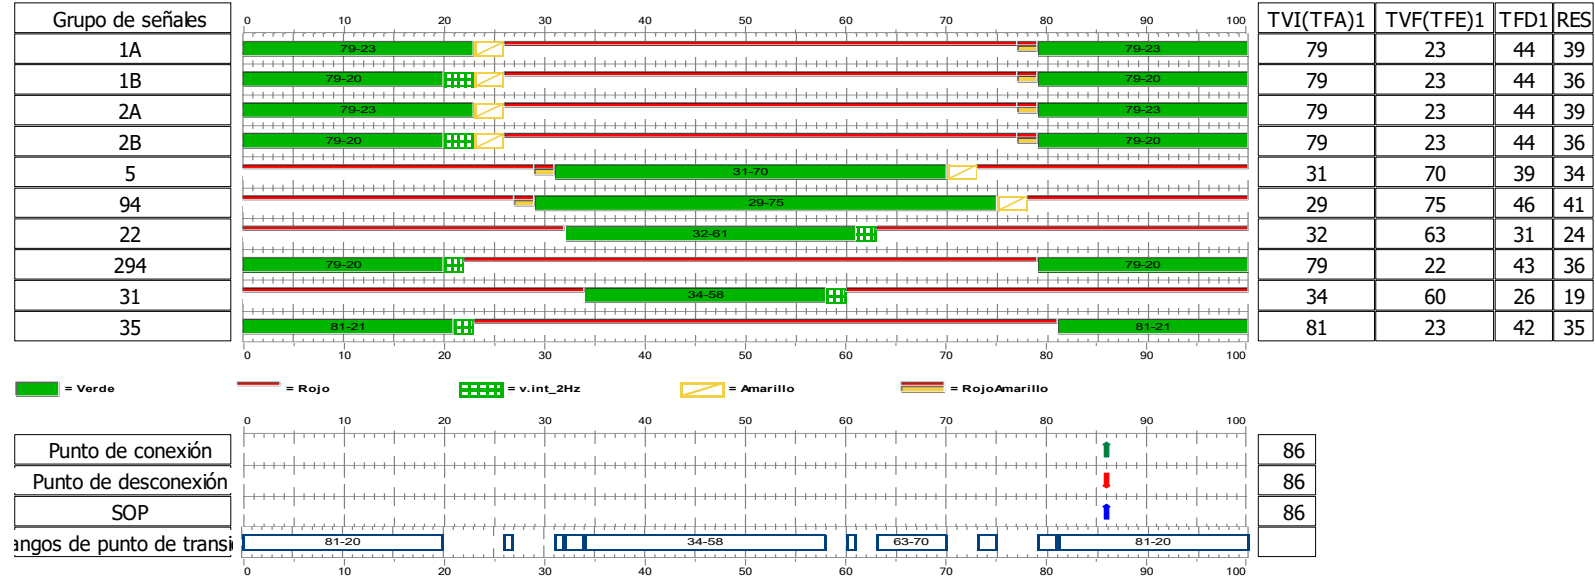


Último usuario / Última actualización = Ing. Alexandra Pataquiva O / 20/11/2025 17:37:18

Externo:	3693	Dirección:	AK 14 X CL 13A S	Zona Auto.:	3605
Encargado:	Ing. Alexandra Pataquiva O.	Versión:	SEMA_3693_VersiónPMT.sop6	Fecha:	20/11/2025 17:40:33
Contrato:	2025 - 380	SDM - Subdirección de Semaforización		Sitraffic Office	


Programas de señal \ PS_4_C900_3693

Ser. no.	O-Nr.	Nombre corto	Nombre	Descripción	Tiempo de Ciclo	No de Com. Dispo.	Tipo	Desfase	Tabla de volúmenes	MT(ZZ)	MDI	MDF	COORDINACION	S-Encendido	S-Off	@Point-in-time values based on
4	4	PS_4_C900_3693	PS_4_C900_3693		100	4	SG	0		MI_C900_3693			1	PC_C900_3693	PD_C900_3693	0

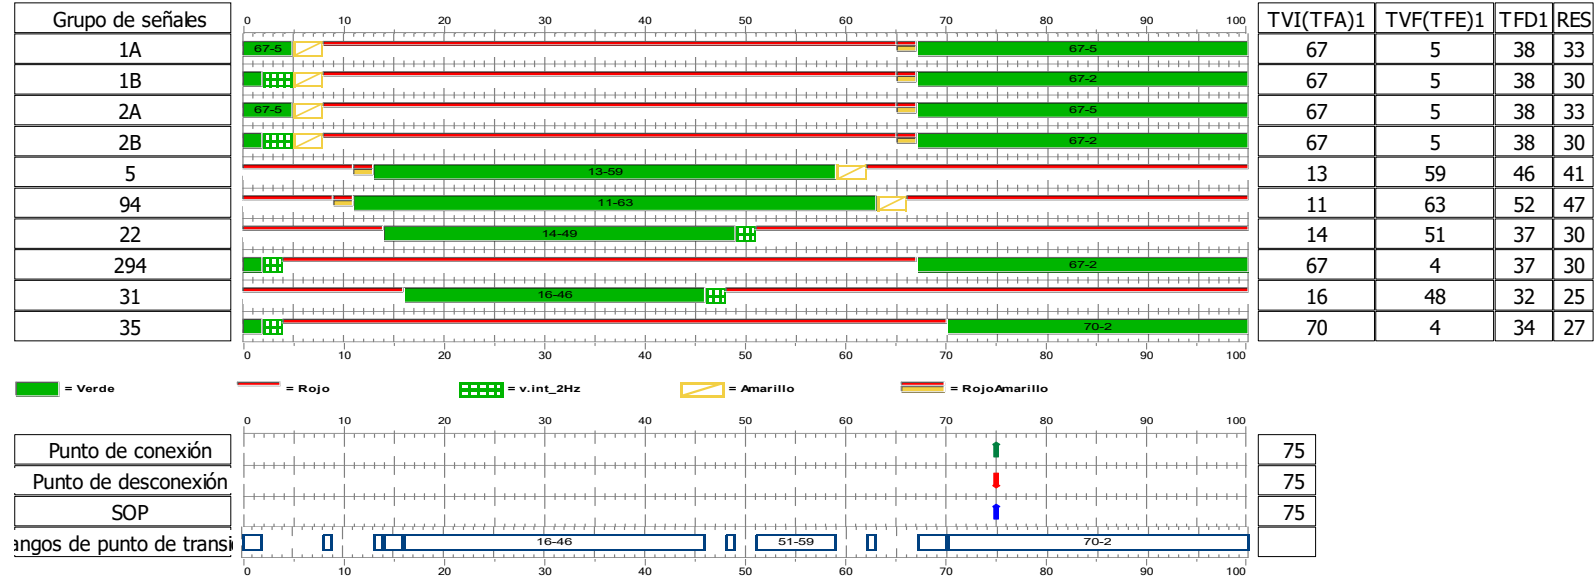

Programas de señal \ PS_5_C900_3693

Ser. no.	O-Nr.	Nombre corto	Nombre	Descripción	Tiempo de Ciclo	No de Com. Dispo.	Tipo	Desfase	Tabla de volúmenes	MT(ZZ)	MDI	MDF	COORDINACION	S-Encendido	S-Off	@Point-in-time values based on
5	5	PS_5_C900_3693	PS_5_C900_3693		90	5	SG	0		MI_C900_3693			1	PC_C900_3693	PD_C900_3693	0

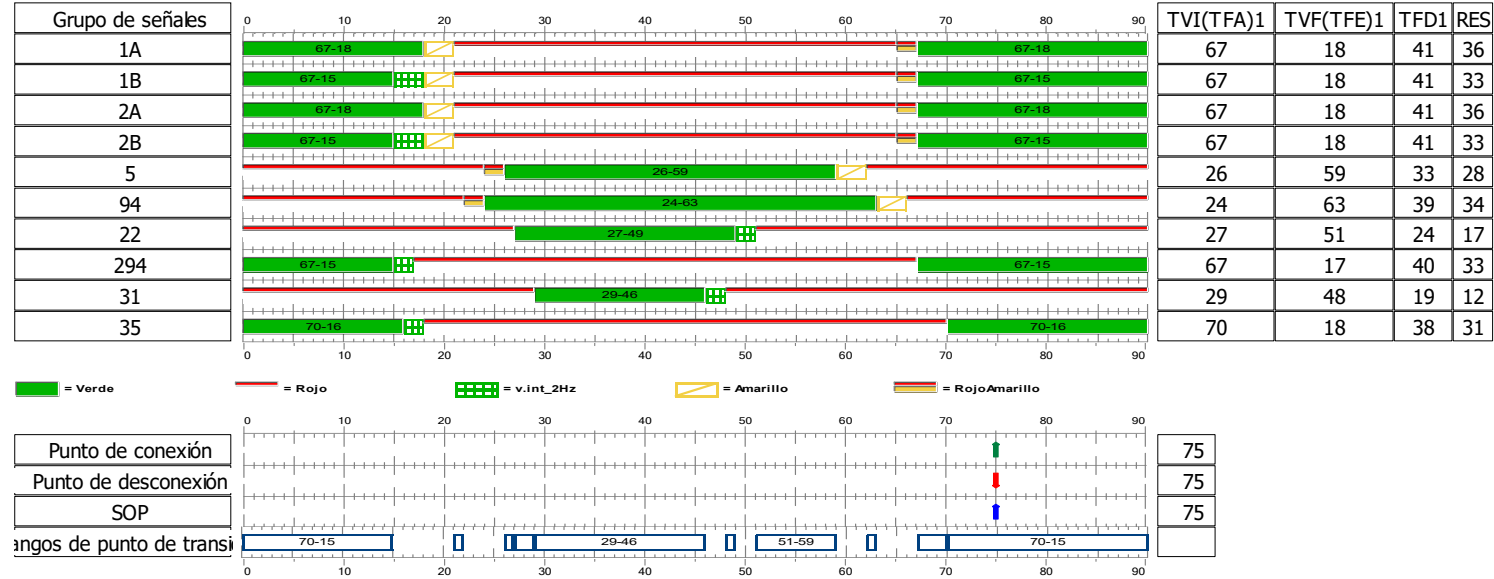


Último usuario / Última actualización = Ing. Alexandra Pataquiva O / 20/11/2025 15:44:18

Externo:	3693	Dirección:	AK 14 X CL 13A S	Zona Auto.:	3605
Encargado:	Ing. Alexandra Pataquiva O.	Versión:	SEMA_3693_VersiónPMT.sop6	Fecha:	20/11/2025 17:40:33
Contrato:	2025 - 380	SDM - Subdirección de Semaforización		Sittraffic Office	

Programas de señal \ PS_6_C900_3693

Ser. no.	O-Nr.	Nombre corto	Nombre	Descripción	Tiempo de Ciclo	No de Com. Dispo.	Tipo	Desfase	Tabla de volúmenes	MT(ZZ)	MDI	MDF	COORDINACION	S-Encendido	S-Off	@Point-in-time values based on
6	6	PS_6_C900_3693	PS_6_C900_3693		90		SG	0		MI_C900_3693			1	PC_C900_3693	PD_C900_3693	0

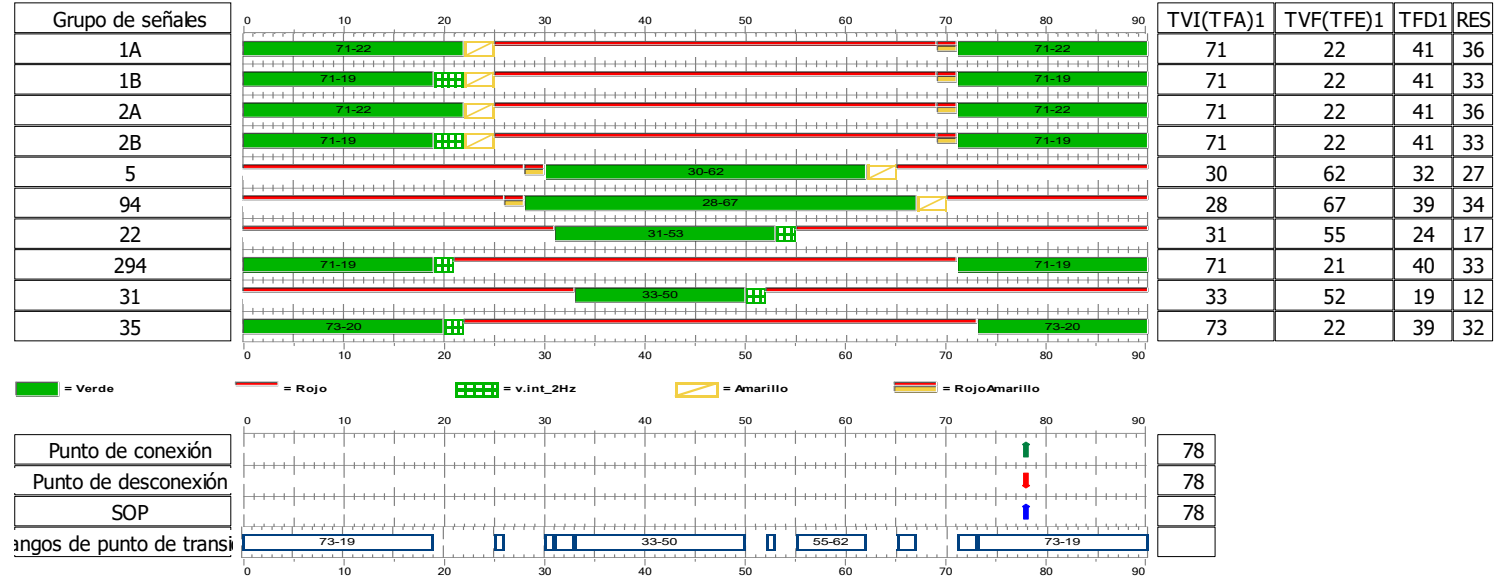


Último usuario / Última actualización = Ing. Alexandra Pataquiva O / 20/11/2025 15:45:38

Externo:	3693	Dirección:	AK 14 X CL 13A S	Zona Auto.:	3605
Encargado:	Ing. Alexandra Pataquiva O.	Versión:	SEMA_3693_VersiónPMT.sop6	Fecha:	20/11/2025 17:40:33
Contrato:	2025 - 380	SDM - Subdirección de Semaforización		Sittraffic Office	

Programas de señal \ PS_7_C900_3693

Ser. no.	O-Nr.	Nombre corto	Nombre	Descripción	Tiempo de Ciclo	No de Com. Dispo.	Tipo	Desfase	Tabla de volúmenes	MT(ZZ)	MDI	MDF	COORDINACION	S-Encendido	S-Off	@Point-in-time values based on
7	7	PS_7_C900_3693	PS_7_C900_3693		75	7	SG	0		MI_C900_3693			1	PC_C900_3693	PD_C900_3693	0

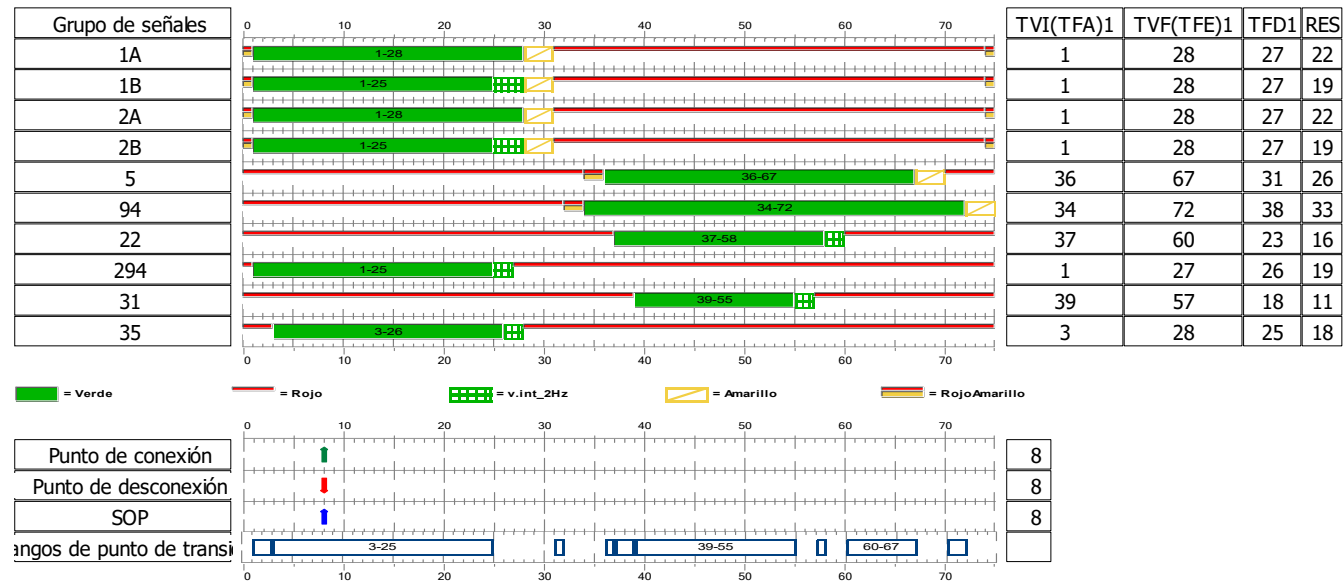


Último usuario / Última actualización = Ing. Alexandra Pataquiva O / 20/11/2025 15:46:37

Externo:	3693	Dirección:	AK 14 X CL 13A S	Zona Auto.:	3605
Encargado:	Ing. Alexandra Pataquiva O.	Versión:	SEMA_3693_VersiónPMT.sop6	Fecha:	20/11/2025 17:40:33
Contrato:	2025 - 380	SDM - Subdirección de Semaforización		Sittraffic Office	

Programas de señal \ PS_8_C900_3693

Ser. no.	O-Nr.	Nombre corto	Nombre	Descripción	Tiempo de Ciclo	No de Com. Dispo.	Tipo	Desfase	Tabla de volúmenes	MTI(ZZ)	MDI	MDF	COORDINACION	S-Encendido	S-Off	@Point-in-time values based on
8	8	PS_8_C900_3693	PS_8_C900_3693		60	8	SG	0		MI_C900_3693			1	PC_C900_3693	PD_C900_3693	0

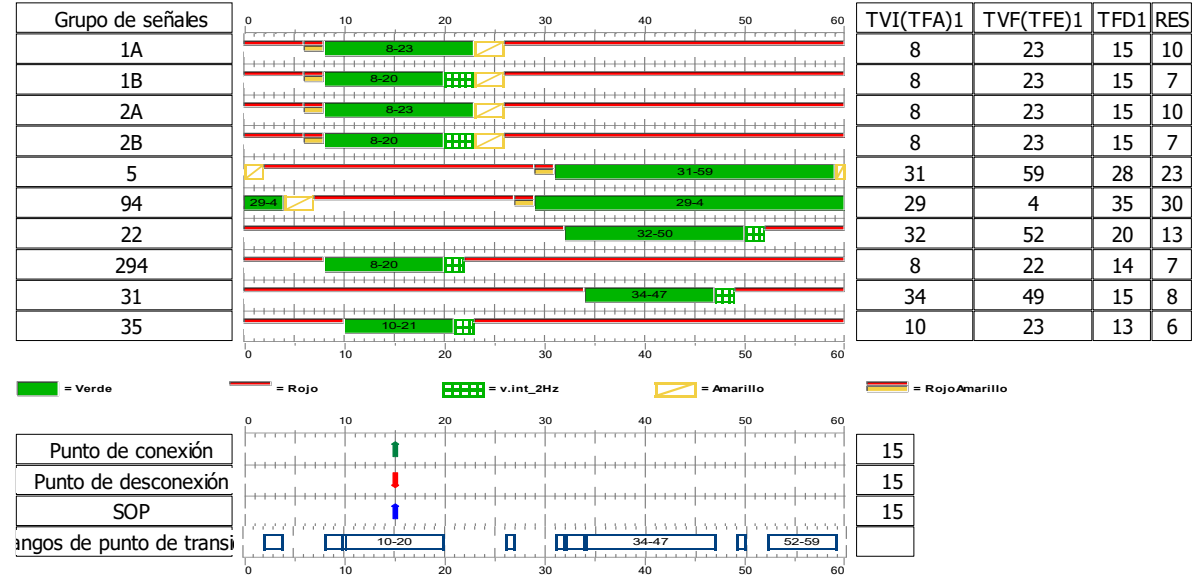


Último usuario / Última actualización = Ing. Alexandra Pataquiva O / 20/11/2025 15:48:06

Externo:	3693	Dirección:	AK 14 X CL 13A S	Zona Auto.:	3605
Encargado:	Ing. Alexandra Pataquiva O.	Versión:	SEMA_3693_VersiónPMT.sop6	Fecha:	20/11/2025 17:40:33
Contrato:	2025 - 380	SDM - Subdirección de Semaforización		Sittraffic Office	

Programas de señal \ PS_9_C900_3693

Ser. no.	O-Nr.	Nombre corto	Nombre	Descripción	Tiempo de Ciclo	No de Com. Dispo.	Tipo	Desfase	Tabla de volúmenes	MT(ZZ)	MDI	MDF	COORDINACION	S-Encendido	S-Off	@Point-in-time values based on
9	9	PS_9_C900_3693	PS_9_C900_3693		100	9	SG	0		MI_C900_3693			1	PC_C900_3693	PD_C900_3693	0

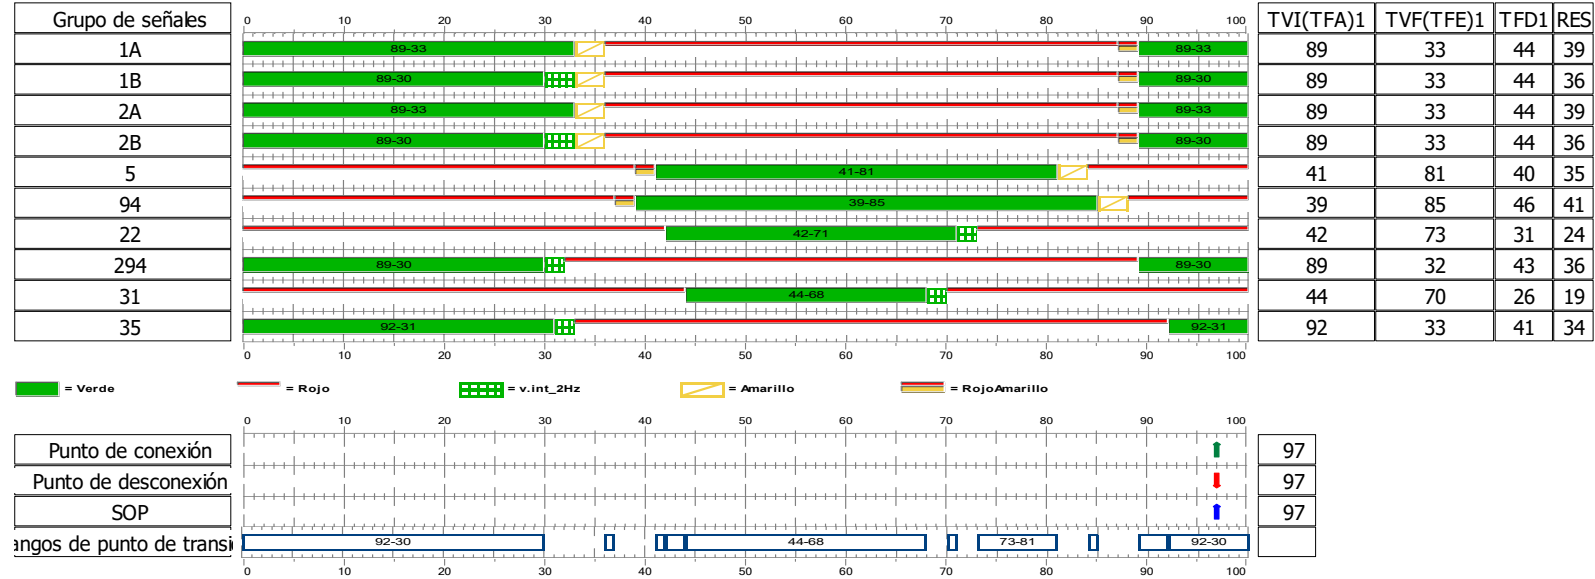


Último usuario / Última actualización = Ing. Alexandra Pataquiva O / 20/11/2025 15:49:56

Externo:	3693	Dirección:	AK 14 X CL 13A S	Zona Auto.:	3605
Encargado:	Ing. Alexandra Pataquiva O.	Versión:	SEMA_3693_VersiónPMT.sop6	Fecha:	20/11/2025 17:40:33
Contrato:	2025 - 380	SDM - Subdirección de Semaforización		Sitraffic Office	

Programas de señal \ PS_10_C900_3693

Ser. no.	O-Nr.	Nombre corto	Nombre	Descripción	Tiempo de Ciclo	No de Com. Dispo.	Tipo	Desfase	Tabla de volúmenes	MTI(ZZ)	MDI	MDF	COORDINACION	S-Encendido	S-Off	@Point-in-time values based on
10	10	PS_10_C900_3693	PS_10_C900_3693		100	10	SG	0		MI_C900_3693			1	PC_C900_3693	PD_C900_3693	0

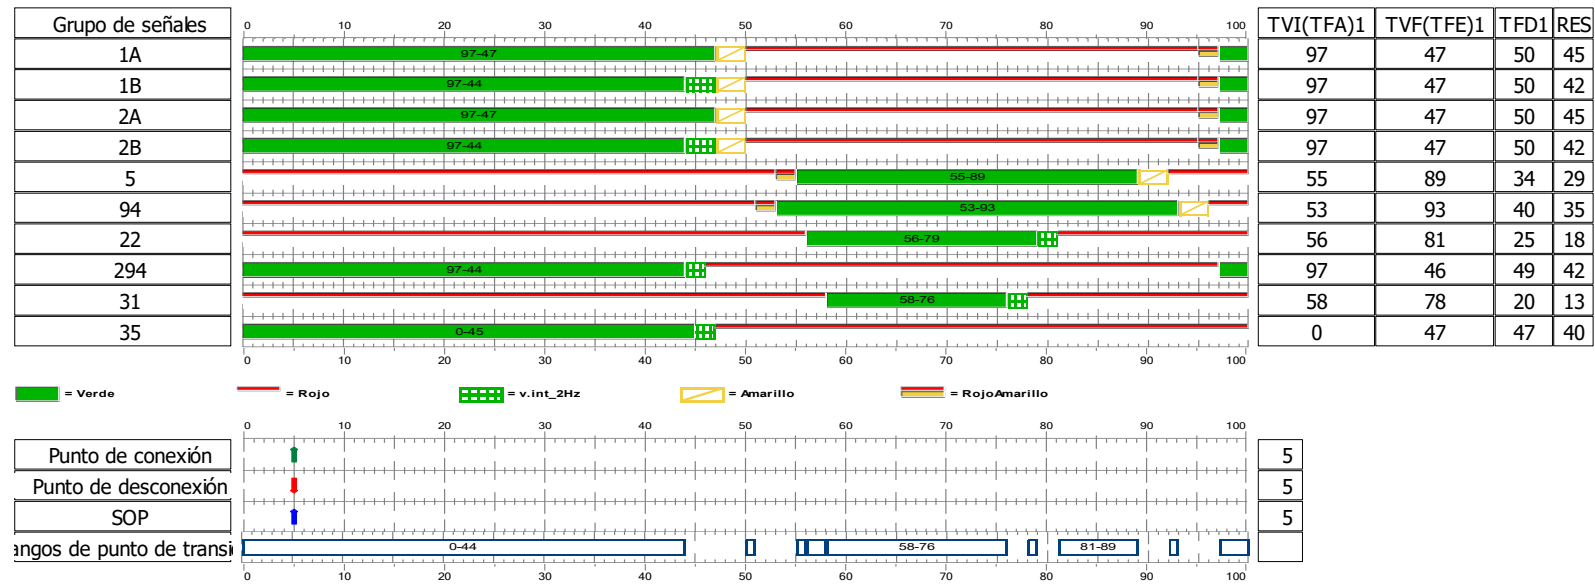


Último usuario / Última actualización = Ing. Alexandra Pataquiva O / 20/11/2025 15:50:39

Externo:	3693	Dirección:	AK 14 X CL 13A S	Zona Auto.:	3605
Encargado:	Ing. Alexandra Pataquiva O.	Versión:	SEMA_3693_VersiónPMT.sop6	Fecha:	20/11/2025 17:40:33
Contrato:	2025 - 380	SDM - Subdirección de Semaforización		Sittraffic Office	

Programas de señal \ PS_11_C900_3693

Ser. no.	O-Nr.	Nombre corto	Nombre	Descripción	Tiempo de Ciclo	No de Com. Dispo.	Tipo	Desfase	Tabla de volúmenes	MTI(ZZ)	MDI	MDF	COORDINACION	S-Encendido	S-Off	@Point-in-time values based on
11	11	PS_11_C900_3693	PS_11_C900_3693		120	11	SG	0		MI_C900_3693			1	PC_C900_3693	PD_C900_3693	0

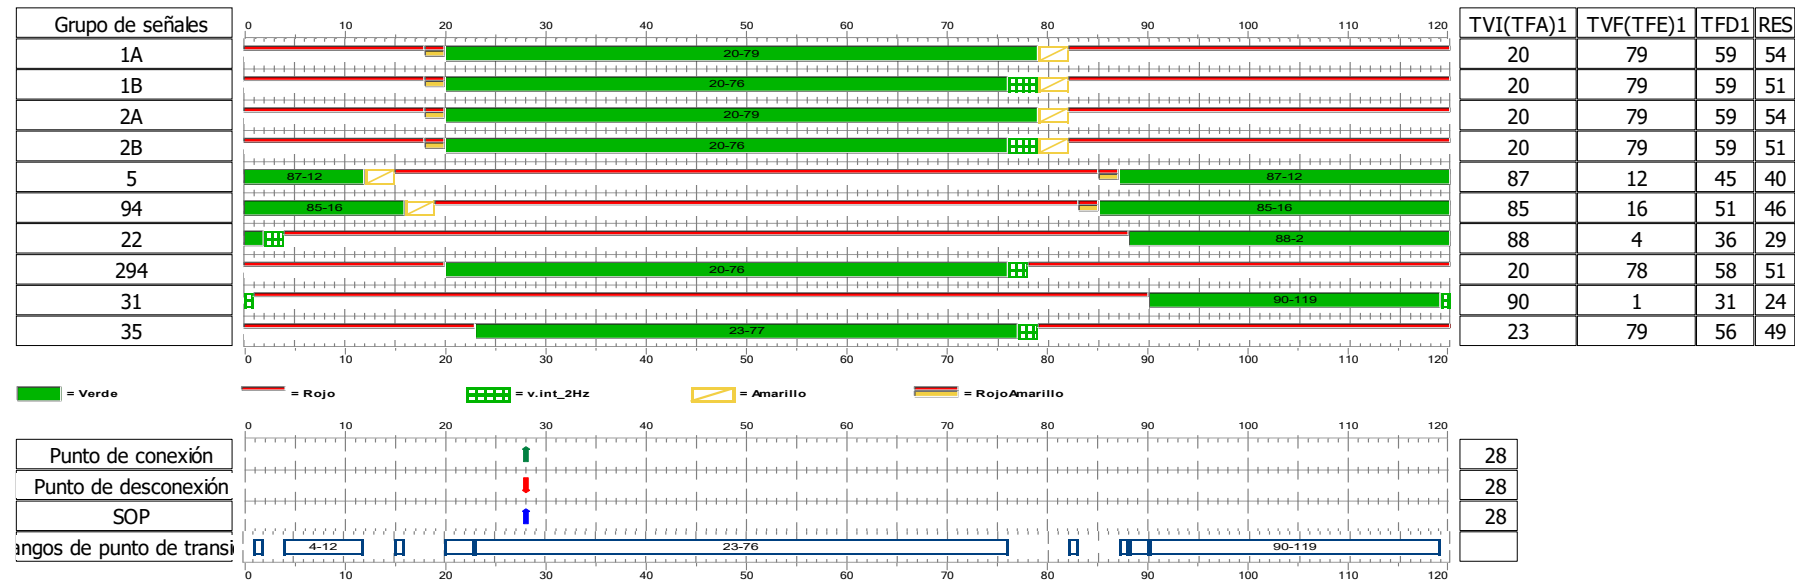


Último usuario / Última actualización = Ing. Alexandra Pataquiva O / 20/11/2025 15:51:07

Externo:	3693	Dirección:	AK 14 X CL 13A S	Zona Auto.:	3605
Encargado:	Ing. Alexandra Pataquiva O.	Versión:	SEMA_3693_VersiónPMT.sop6	Fecha:	20/11/2025 17:40:33
Contrato:	2025 - 380	SDM - Subdirección de Semaforización		Sittraffic Office	

Programas de señal \ PS_12_C900_3693

Ser. no.	O-Nr.	Nombre corto	Nombre	Descripción	Tiempo de Ciclo	No de Com. Dispo.	Tipo	Desfase	Tabla de volúmenes	MTI(ZZ)	MDI	MDF	COORDINACION	S-Encendido	S-Off	@Point-in-time values based on
12	12	PS_12_C900_3693	PS_12_C900_3693		120	12	SG	0		MI_C900_3693			1	PC_C900_3693	PD_C900_3693	0

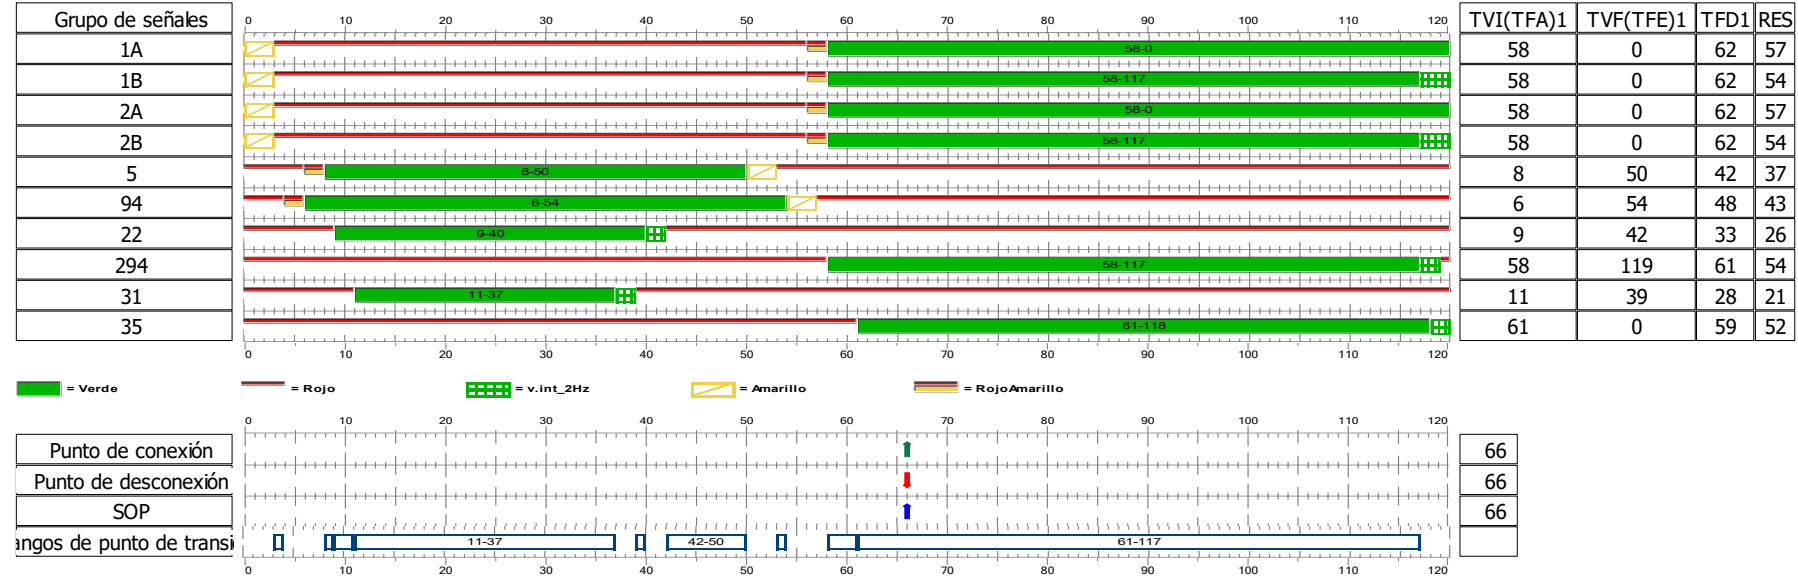


Último usuario / Última actualización = Ing. Alexandra Pataquiva O / 20/11/2025 15:51:55

Externo:	3693	Dirección:	AK 14 X CL 13A S	Zona Auto.:	3605
Encargado:	Ing. Alexandra Pataquiva O.	Versión:	SEMA_3693_VersiónPMT.sop6	Fecha:	20/11/2025 17:40:33
Contrato:	2025 - 380	SDM - Subdirección de Semaforización		Sittraffic Office	

Programas de señal \ PS_13_C900_3693

Ser. no.	O-Nr.	Nombre corto	Nombre	Descripción	Tiempo de Ciclo	No de Com. Dispo.	Tipo	Desfase	Tabla de volúmenes	MTI(ZZ)	MDI	MDF	COORDINACION	S-Encendido	S-Off	@Point-in-time values based on
13	13	PS_13_C900_3693	PS_13_C900_3693		120	13	SG	0		MI_C900_3693			1	PC_C900_3693	PD_C900_3693	0

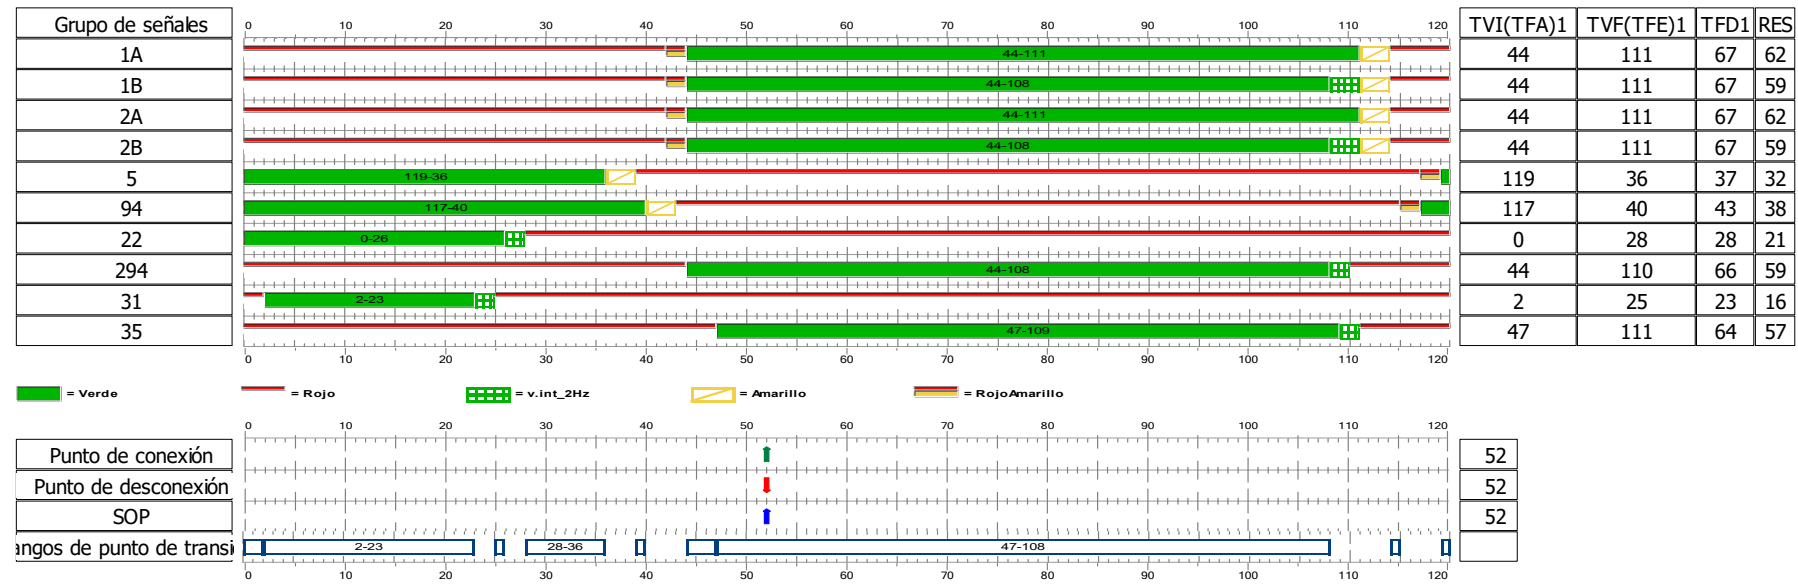

Último usuario / Última actualización = Ing. Alexandra Pataquiva O / 20/11/2025 15:52:50

Externo:	3693	Dirección:	AK 14 X CL 13A S	Zona Auto.:	3605
Encargado:	Ing. Alexandra Pataquiva O.	Versión:	SEMA_3693_VersiónPMT.sop6	Fecha:	20/11/2025 17:40:33
Contrato:	2025 - 380	SDM - Subdirección de Semaforización		Sittraffic Office	